


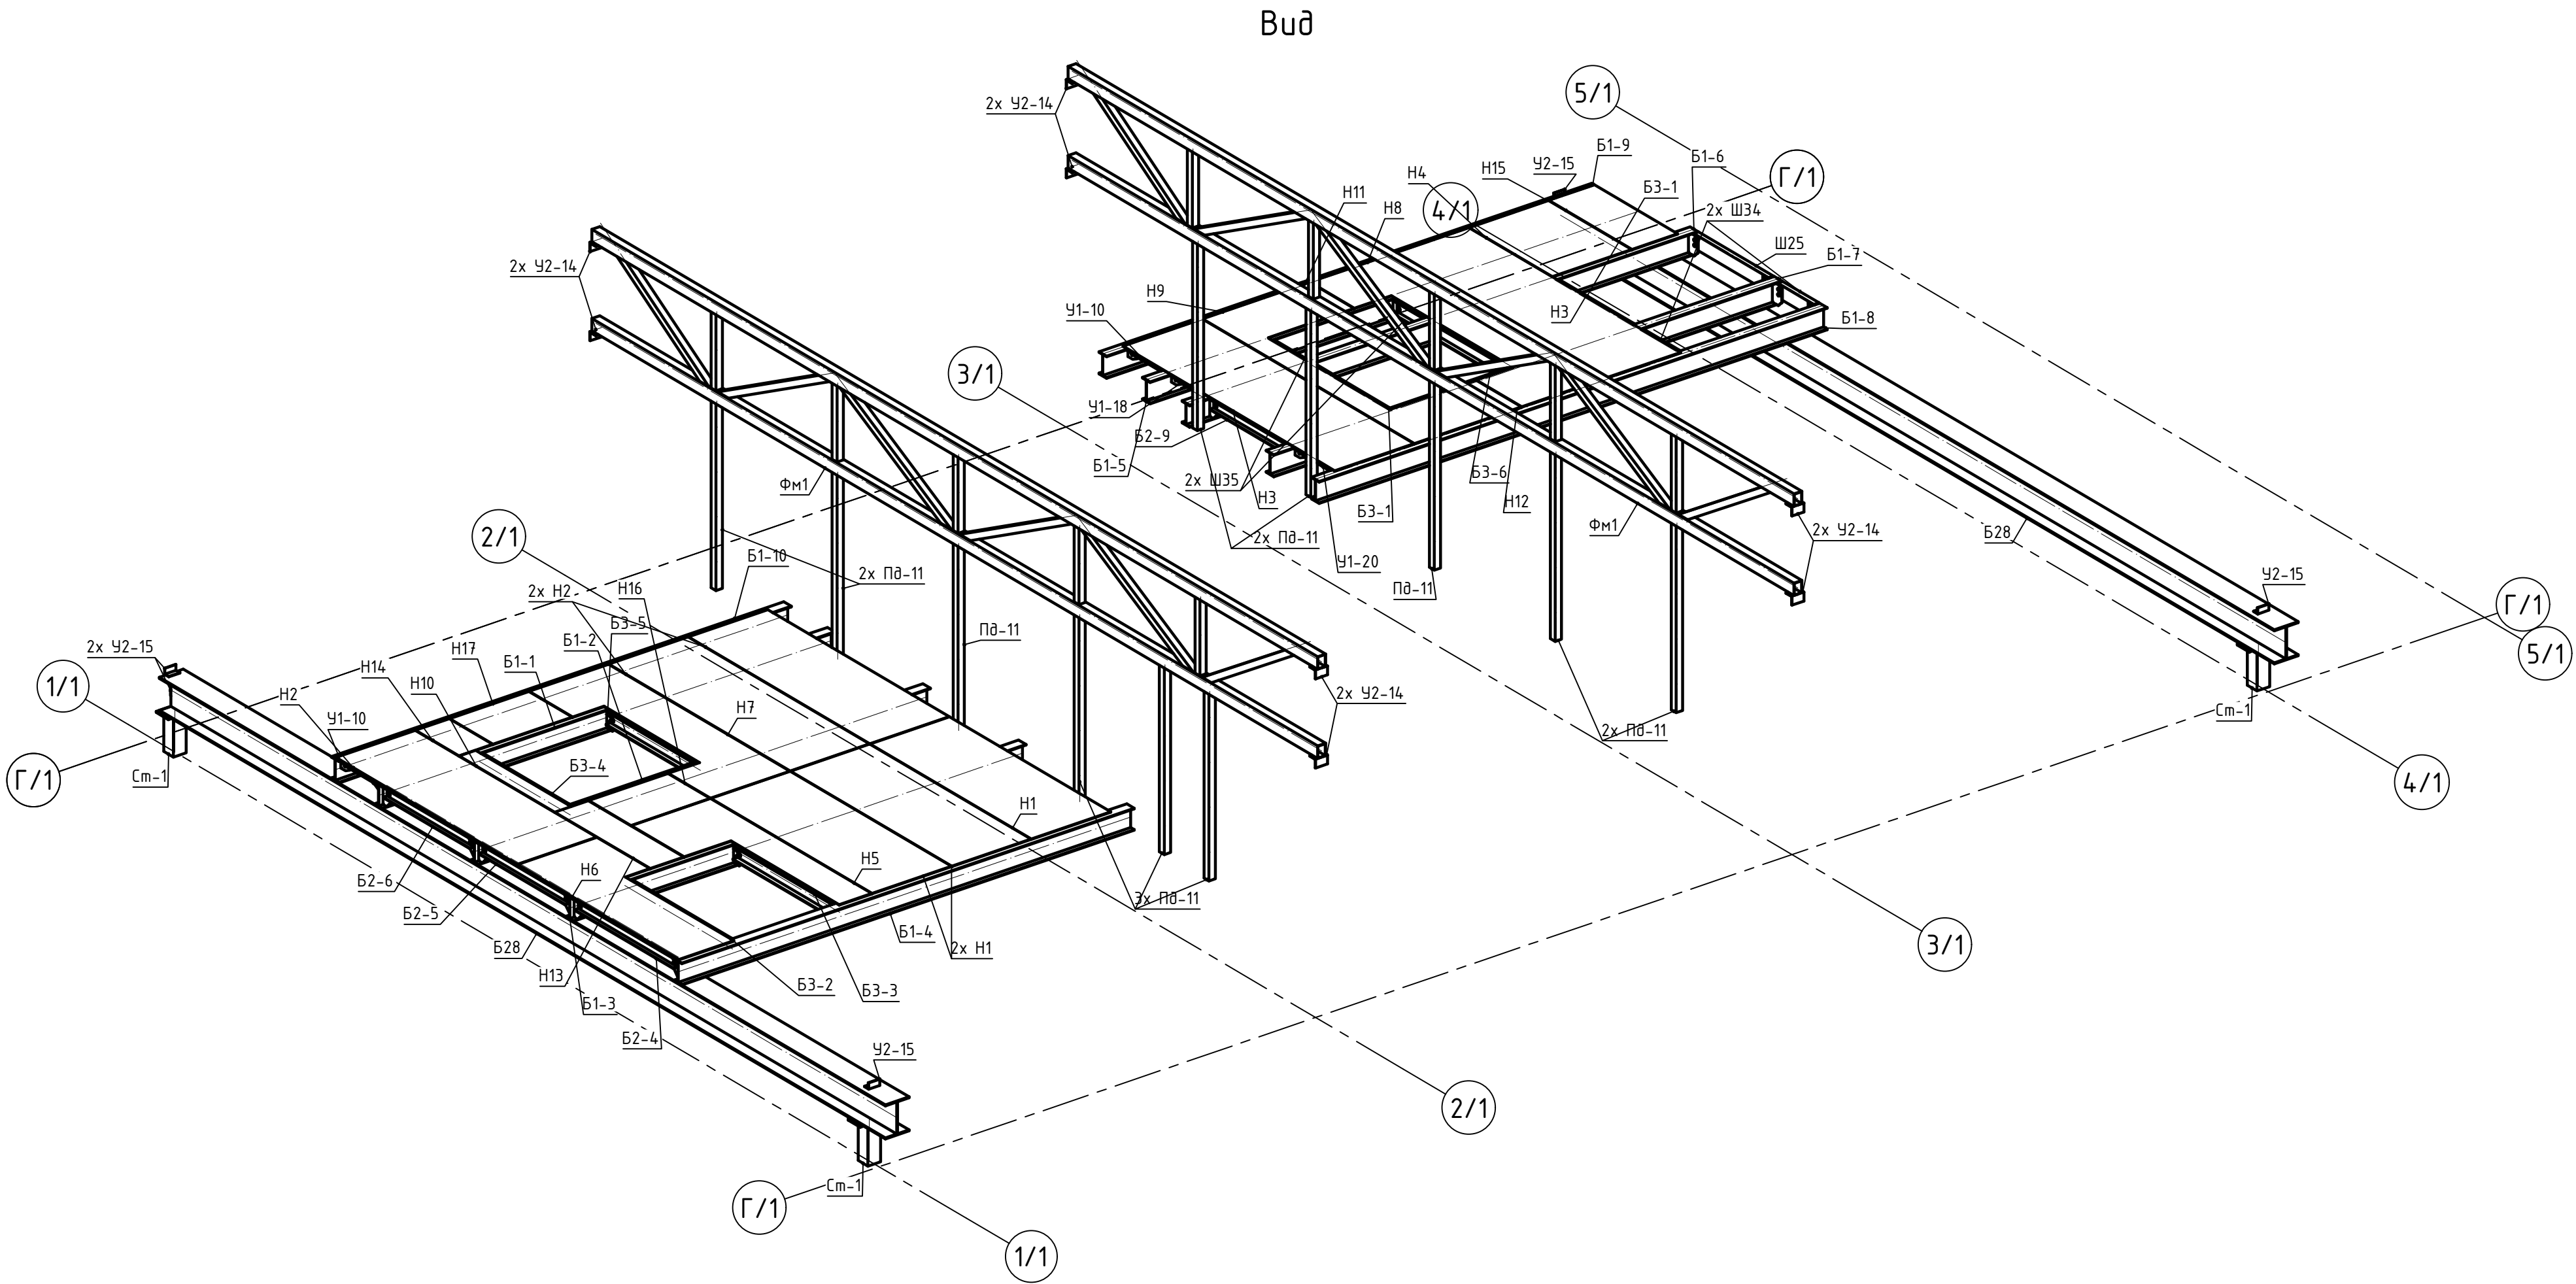

						927-26. Устройство площадок под рамы оборудования на чердаке компрессорной в осях Г/1-Д/1 - 1/1-5/1				
								Стадия	Масса	Масштаб
Изм.	Колуч	Лист	Ндок.	Подпись	Дата	Настил,Нет,Пластина-ребро,Стойка,Уголок,Ферма				1:50
Гл.Инженер		Михнюк Д.В.			09.06.2026					
Нач. отдела		Иванюк В.С.			09.06.2026					
					09.06.2026			Лист 01	Листов	
Н.Контр.		Иванюк В.С.			09.06.2026			ООО "АльденаГрупп"		
					09.06.2026					
Разработал		Иванюк В.С.			09.06.2026					

Требуется изготовить			
Отпр. марка	Кол-во, шт.	Масса, кг	
		шт.	общ.
Б1-1	1	173.82	173.82
Б1-2	1	184.67	184.67
Б1-3	1	187.59	187.59
Б1-4	1	167.12	167.12
Б1-5	1	184.85	184.85
Б1-6	1	193.69	193.69
Б1-7	1	192.31	192.31
Б1-8	1	177.55	177.55
Б1-9	1	172.05	172.05
Б1-10	1	157.58	157.58
Б2-1	5	16.73	83.63
Б2-2	3	18.93	56.79
Б2-3	2	16.73	33.45
Б2-4	1	17.76	17.76
Б2-5	1	15.55	15.55
Б2-6	1	15.55	15.55
Б2-7	1	14.02	14.02
Б2-8	1	16.95	16.95
Б2-9	1	13.71	13.71
Б2-10	1	15.55	15.55
Б2-11	1	15.55	15.55
Б2-12	1	17.76	17.76
Б3-1	2	18.69	37.38
Б3-2	1	24.03	24.03
Б3-3	1	24.03	24.03
Б3-4	1	21.02	21.02
Б3-5	1	21.02	21.02
Б3-6	1	18.69	18.69
Б28	2	1073.83	2147.66
Н1	3	44.18	132.53
Н2	3	49.69	149.08
Н3	2	57.97	115.95
Н4	1	22.78	22.78
Н5	1	44.18	44.18
Н6	1	44.18	44.18
Н7	1	49.69	49.69
Н8	1	57.97	57.97
Н9	1	57.97	57.97
Н10	1	5.42	5.42
Н11	1	4.21	4.21
Н12	1	4.3	4.3
Н13	1	11.12	11.12
Н14	1	5.06	5.06
Н15	1	13.11	13.11
Н16	1	11.59	11.59
Н17	1	11.9	11.9
Пд-11	11	19.56	215.11

продолжение.

Требуется изготовить			
Отпр. марка	Кол-во, шт.	Масса, кг	
		шт.	общ.
См-1	4	17.85	71.41
У1-10	15	3.02	45.32
У1-17	6	4.96	29.77
У1-18	6	2.67	16.01
У1-20	5	3.18	15.92
У1-29	2	4.9	9.81
У1-30	2	3.11	6.22
У1-31	2	3.08	6.16
У1-36	1	5.97	5.97
У1-37	1	4.88	4.88
У1-38	1	4.87	4.87
У1-39	1	3.16	3.16
У1-40	1	2.8	2.8
У1-41	1	1.85	1.85
У1-42	1	1.73	1.73
У2-14	8	1.63	13.08
У2-15	8	0.76	6.09
Фм1	2	494.41	988.82
Ш25	1	17.73	17.73
Ш34	2	8.55	17.1
Ш35	2	7.19	14.37
Итого:		6640.52	

продолжение.

Площадь окраски			
Отпр. марка	Кол-во марок	Площадь, м. кв.	
		шт.	общ.
Б1-1	1	6.24	6.24
Б1-2	1	6.53	6.53
Б1-3	1	6.62	6.62
Б1-4	1	6.04	6.04
Б1-5	1	6.68	6.68
Б1-6	1	7.02	7.02
Б1-7	1	6.98	6.98
Б1-8	1	6.51	6.51
Б1-9	1	6.28	6.28
Б1-10	1	5.76	5.76
Б2-1	5	0.65	3.27
Б2-2	3	0.74	2.23
Б2-3	2	0.65	1.31
Б2-4	1	0.71	0.71
Б2-5	1	0.62	0.62
Б2-6	1	0.62	0.62
Б2-7	1	0.54	0.54
Б2-8	1	0.66	0.66
Б2-9	1	0.55	0.55
Б2-10	1	0.62	0.62
Б2-11	1	0.62	0.62
Б2-12	1	0.71	0.71
Б3-1	2	0.71	1.42
Б3-2	1	0.91	0.91
Б3-3	1	0.91	0.91
Б3-4	1	0.8	0.8
Б3-5	1	0.8	0.8
Б3-6	1	0.71	0.71
Б28	2	22.86	45.73
Н1	3	5.37	16.11
Н2	3	6.04	18.12
Н3	2	7.04	14.09
Н4	1	2.77	2.77
Н5	1	5.37	5.37
Н6	1	5.37	5.37
Н7	1	6.04	6.04
Н8	1	7.04	7.04
Н9	1	7.04	7.04
Н10	1	0.67	0.67
Н11	1	0.52	0.52
Н12	1	0.53	0.53
Н13	1	1.36	1.36
Н14	1	0.62	0.62
Н15	1	1.6	1.6
Н16	1	1.42	1.42
Н17	1	1.45	1.45
Пд-11	11	0.64	7.07

продолжение.

Площадь окраски			
Отпр. марка	Кол-во марок	Площадь, м. кв.	
		шт.	общ.
См-1	4	0.44	1.77
У1-10	15	0.15	2.29
У1-17	6	0.25	1.5
У1-18	6	0.13	0.81
У1-20	5	0.16	0.8
У1-29	2	0.25	0.5
У1-30	2	0.16	0.31
У1-31	2	0.16	0.31
У1-36	1	0.3	0.3
У1-37	1	0.25	0.25
У1-38	1	0.25	0.25
У1-39	1	0.16	0.16
У1-40	1	0.14	0.14
У1-41	1	0.09	0.09
У1-42	1	0.09	0.09
У2-14	8	0.06	0.47
У2-15	8	0.04	0.31
Фм1	2	16.09	32.17
Ш25	1	0.68	0.68
Ш34	2	0.33	0.65
Ш35	2	0.27	0.55
Площадь итога:		270.01	

Выборка металла			
Сечение	Вес, кг	Марка стали	Примечание
l25Б1	1544.8	С245	
l40Ш1	2126.4	С245	
L100x7	12.95	С245	
L70x5	158.95	С245	
† 10	201.08	С245	
† 12	26.38	С245	
† 5	733.7	ПВ 506	
† 8	57.6	С245	
Гн. 160x5	44.32	С245	
Гн. 80x4	508.01	С245	
Гн. 140x100x4	684	С245	
С12П	288.26	С245	
С16П	188.32	С245	
На сварные швы	65.75		
Итого:	6640.52		

Ведомость метизов						
Наименование и диаметр	Длина, мм	Кол-во, шт.	Масса, кг.		Класс прочности	Примечание
			шт.	общ.		
Болт М16 – 6gx55.58	55	214	0.11	25,94	5.8	7798–70
Гайка М16 6Н.5 ГОСТ	0	428	0.04	16.1	5	5915–70
Шайба С.16.01.08кп.016	0	428	0.01	4.7	5	11371–78

						927-26. Устройство площадок под рамы оборудования на чердаке компрессорной в осях Г/1-Д/1 – 1/1-5/1				
								Стадия	Масса	Масштаб
Изм.	Кол.уч	Лист	Ндок.	Подпись	Дата	Настил,Нет,Пластина-ребро,Стойка,Уголок,Ферма				1:50
Гл.Инженер		Михнюк Д.В.		09.06.2026						
Нач. отдела		Иванюк В.С.		09.06.2026						
					09.06.2026			Лист 01	Листов	
Н.Контр.		Иванюк В.С.		09.06.2026		ООО “АльденаГрупп”				
				09.06.2026						
Разработал		Иванюк В.С.		09.06.2026						