


Вид

Ведомость металлоб					
Наименование и диаметр	Длина, мм	Кол-во, шт	Масса, кг, общ.	Класс прочности	Примечание
Болт М20 – 6дх70.88	70	280	61	8.8	7798–70
Гайка М20 6Н.5 ГОСТ	0	560	37	5	5915–70
Шайба С.20.01.08кп.016	0	560	13	5	11371–78
Высокопр. болт М20 – 6дх75.109	75	1000	270	10.9	ГОСТ Р 52643–2006
Высокопр. гайка М20 6Н.5	0	1000	106		ГОСТ Р 52645–2006
Шайба С.20.01.08кп.016	0	2000	56		ГОСТ 22355–77
Гайка М36		168	75		база колонн для анкера
Шайба М36		112	13.2		база колонн для анкера

Требуется изготовить			
Отпр. марка	Кол-во, шт.	Масса, кг	
		шт.	общ.
Б–1	7	1863.77	13046.37
Б–2	11	1050.72	11557.91
К–1	10	1338.73	13387.31
К–2	2	1401.35	2802.7
К–3	2	1401.35	2802.7
К–4	1	1533.52	1533.52
К–5	1	1533.52	1533.52
К–6	1	1543.9	1543.9
К–7	1	1542.14	1542.14
К–8	1	1630.79	1630.79
К–9	1	1632.55	1632.55
К–10	1	1543.9	1543.9
К–11	1	1531.76	1531.76
К–12	1	1542.14	1542.14
К–13	1	1543.9	1543.9
К–14	1	1630.79	1630.79
К–15	1	1632.55	1632.55
К–16	1	1543.9	1543.9
К–17	1	1531.76	1531.76
Пл23	112	1.37	153.45
Пл26	56	7.33	410.25
Пл32	28	19.98	559.43
Пл33	28	26.64	745.91
Р–1	12	178.76	2145.12
Р–2	4	67.5	269.99
Р–3	4	178.76	715.04
СВ–1	8	105.52	844.15
СВ–2	8	109.56	876.48
СВ–3	4	154.43	617.72
СВ–4	2	222.1	444.19
СВ–5	2	223.99	447.99
Сз1	84	1.47	123.16
Итого:		73867.01	

Выборка металла			
Сечение	Вес, кг	Марка стали	Примечание
120Ш1	3099.17	С245	
140Ш2	11443.47	С245	
160Ш2	46433.08	С245	
RD16	121.94	S500	
† 12	4250.04	С245	
† 14	1915.25	С245	
† 20	830.84	С245	
† 30	2474.07	С245	
† 5	70.84	С245	
Гн. 160х5.5	2496.95	С245	
На старые швы:	731.36		
Итого:	73867.01		

						№929-26-КМД (05-09/24-КМ). "Реконструкция здания главного корпуса с инвентарным номером 110/С-97826 производственного филиала ОАО "Савушкин продукт" г.Барановичи, ул. 50 лет БССР, 51/1"			
						Стадия		Масса	Масштаб
Изм.	Колуч	Лист	Идк.	Подпись	Дата				1:50
Г.Инженер			Михаил Д.В.		25.06.2026				
Нач. отдела			Иванчик В.С.		25.06.2026				
Н.Контр.			Иванчик В.С.		25.06.2026	Лист 100		Листов	
Разработчик			Иванчик В.С.		25.06.2026				000 "Альдега групп"

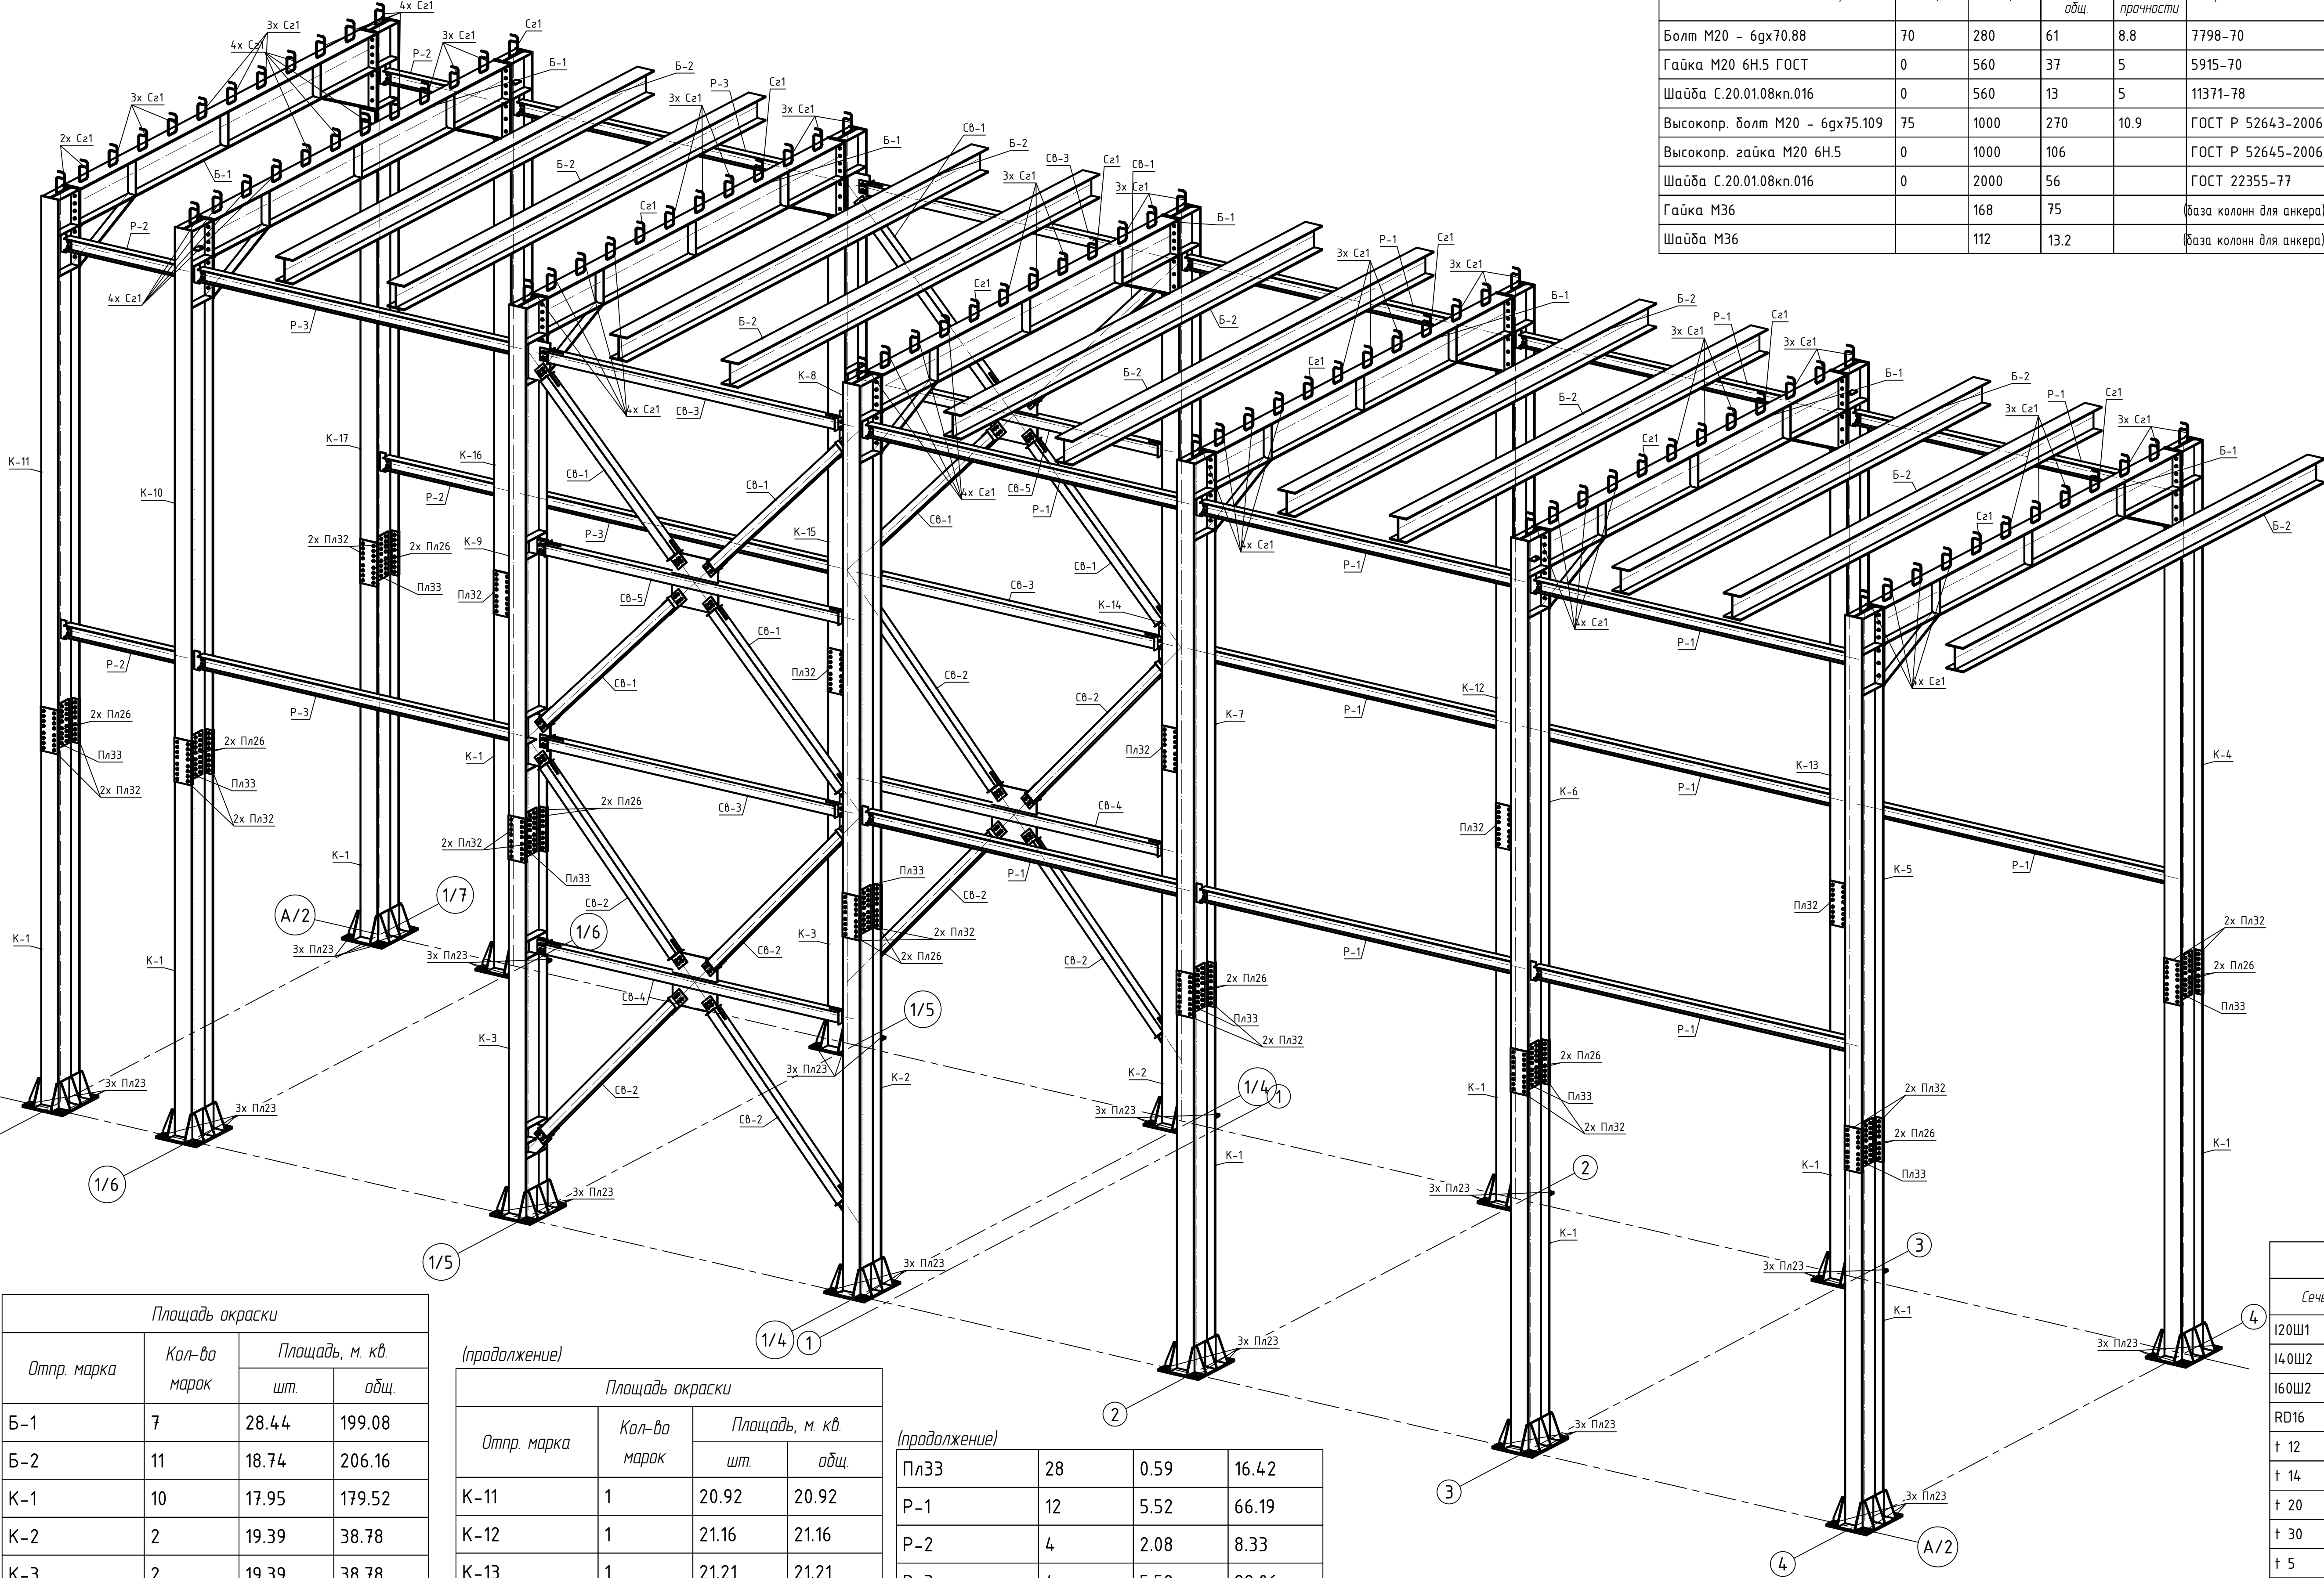

Площадь окраски			
Отпр. марка	Кол-во марок	Площадь, м. кв.	
		шт.	общ.
Б–1	7	28.44	199.08
Б–2	11	18.74	206.16
К–1	10	17.95	179.52
К–2	2	19.39	38.78
К–3	2	19.39	38.78
К–4	1	20.96	20.96
К–5	1	20.96	20.96
К–6	1	21.21	21.21
К–7	1	21.16	21.16
К–8	1	23.16	23.16
К–9	1	23.2	23.2
К–10	1	21.21	21.21

(продолжение) Площадь окраски			
Отпр. марка	Кол-во марок	Площадь, м. кв.	
		шт.	общ.
К–11	1	20.92	20.92
К–12	1	21.16	21.16
К–13	1	21.21	21.21
К–14	1	23.16	23.16
К–15	1	23.2	23.2
К–16	1	21.21	21.21
К–17	1	20.92	20.92
Пл23	112	0.03	3.87
Пл26	56	0.17	9.71
Пл32	28	0.44	12.43

(продолжение)			
Пл33	28	0.59	16.42
Р–1	12	5.52	66.19
Р–2	4	2.08	8.33
Р–3	4	5.52	22.06
СВ–1	8	2.57	20.56
СВ–2	8	2.67	21.32
СВ–3	4	3.72	14.89
СВ–4	2	5.19	10.39
СВ–5	2	5.23	10.47
Сз1	84	0.05	4.1
Площадь итого: 1186.69			

Всех инф. N
Подпись и дата
Инд. М. подл.