




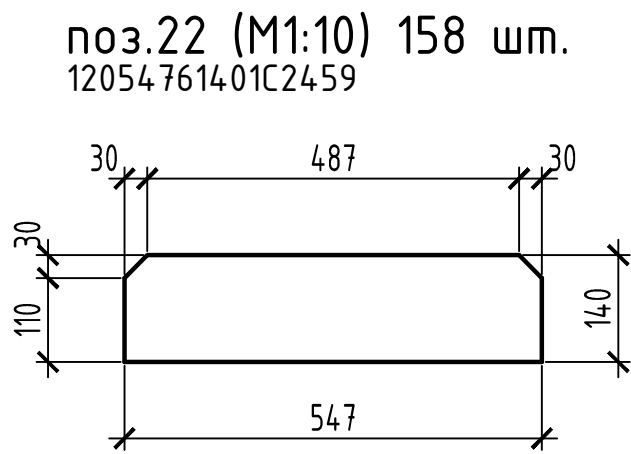


поз.23 (M1:10) 112 шт.
12012061201C2459

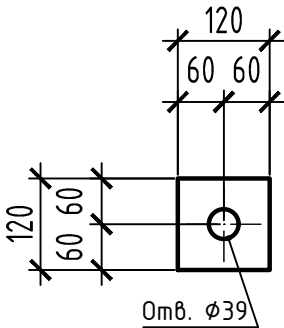


поз.24 (M1:10) 96 шт.
502006941C2459

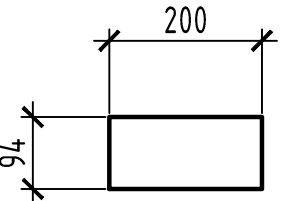


поз.25 (M1:10) 56 шт.
14040061951C2459

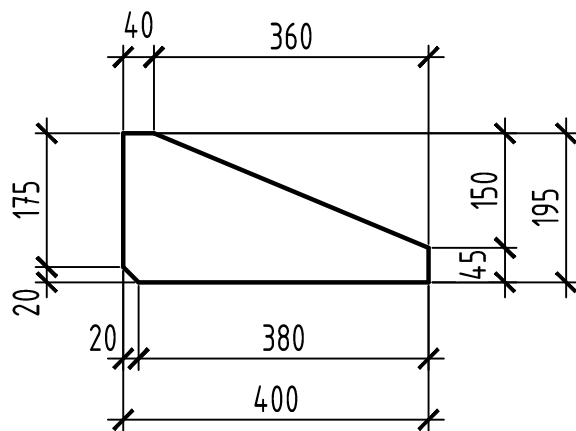


поз.26 (M1:10) 56 шт.
12070061101C2459

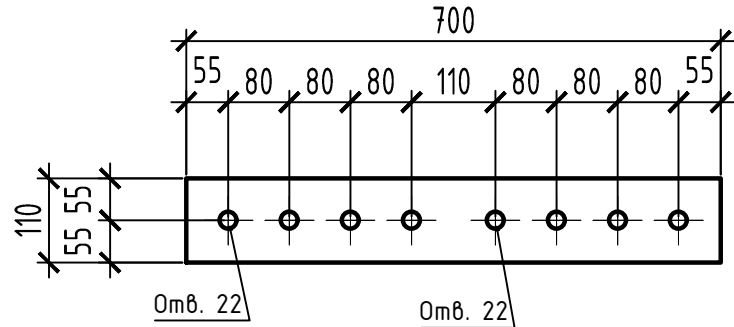


поз.27 (M1:10) 48 шт.
12041062001C2459

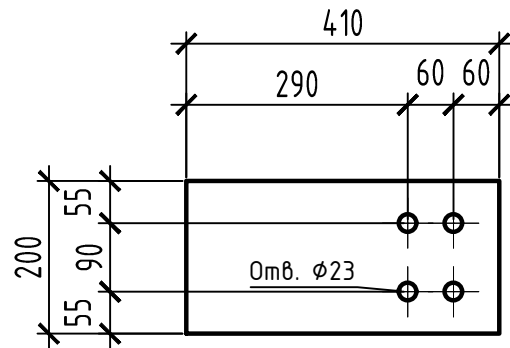


поз.28 (M1:10) 32 шт.
12029561851C2459

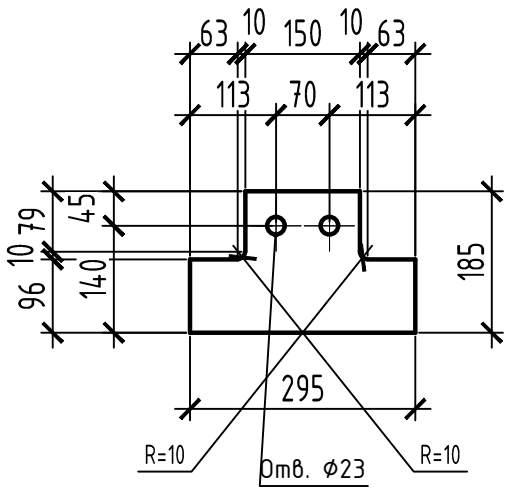


поз.30 (M1:10) 28 шт.
14040061961C2459

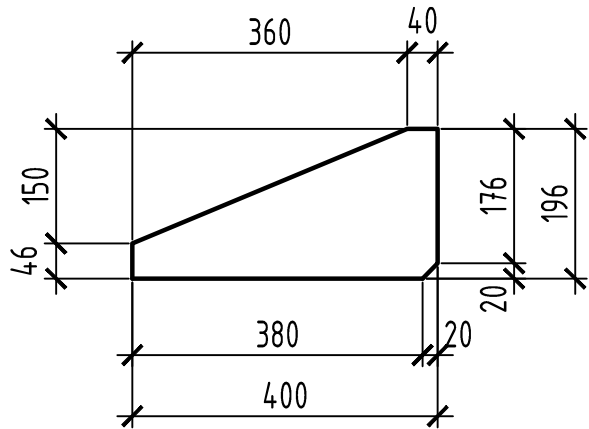


поз.31 (M1:10) 28 шт.
14097064001C2459

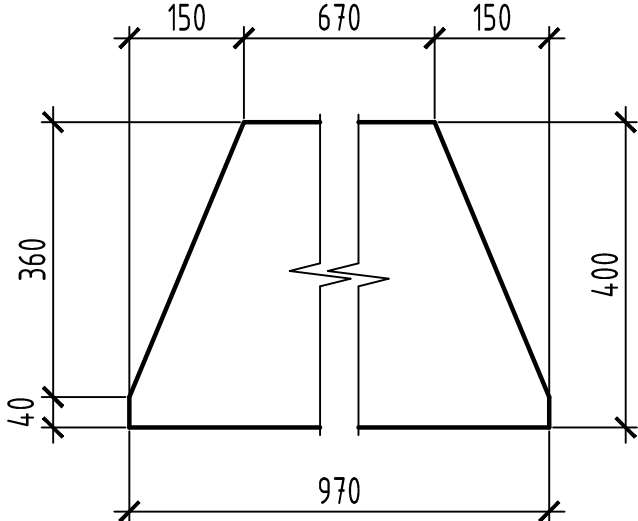


поз.33 (M1:10) 28 шт.
12070064001C2459

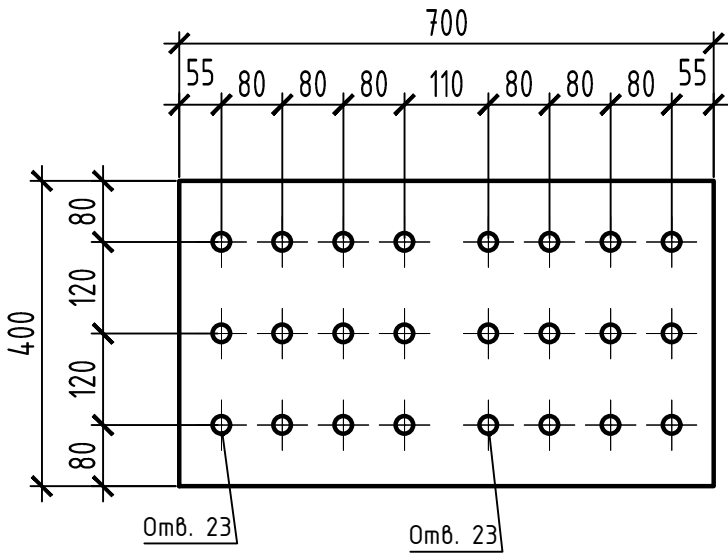


поз.34 (M1:10) 16 шт.
12026761401C2459

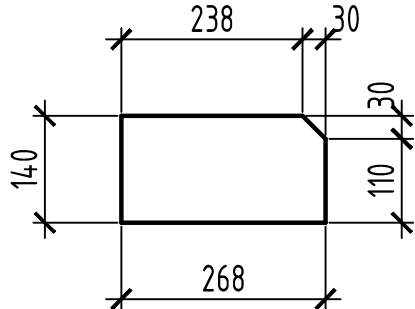


поз.35 (M1:10) 14 шт.
30026062001C2459

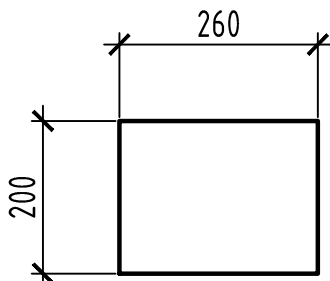


поз.39 (M1:10) 8 шт.
12033662601C2459

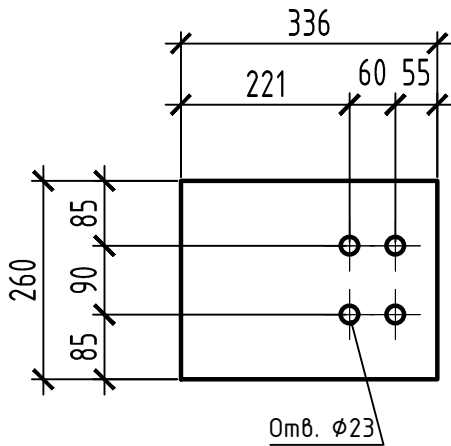


поз.36 (M1:10) 14 шт.
30097067201C2459

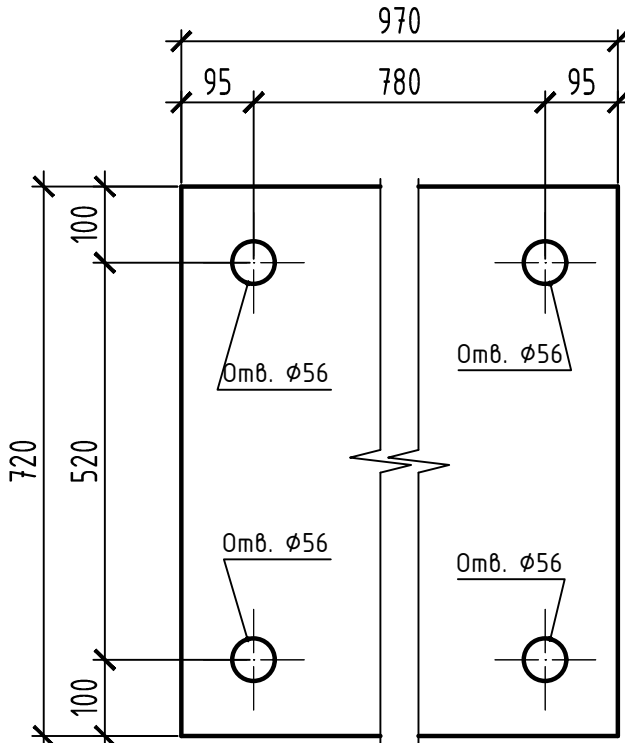


поз.37 (M1:10) 14 шт.
200126063001C2459

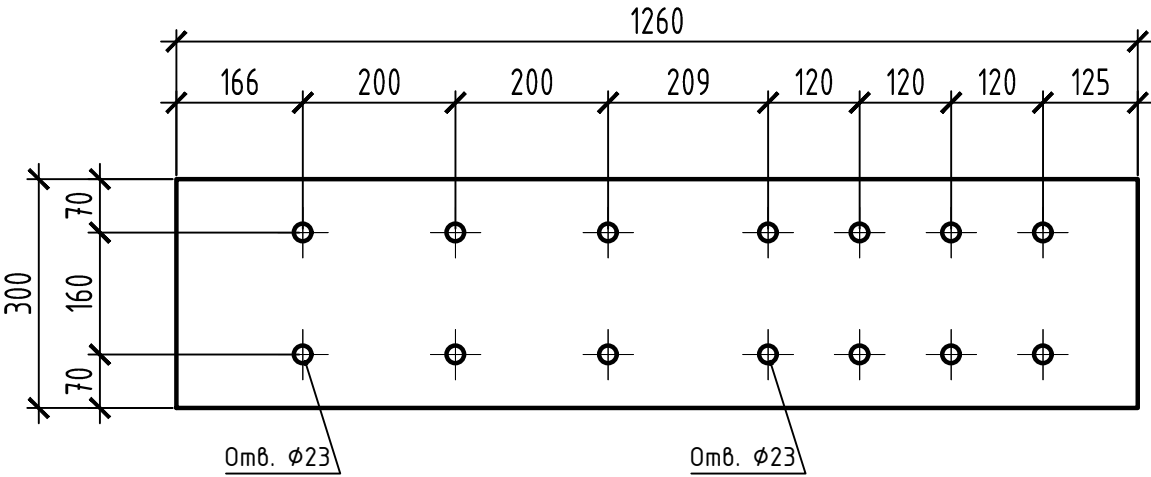


поз.38 (M1:10) 8 шт.
12029561851C2459

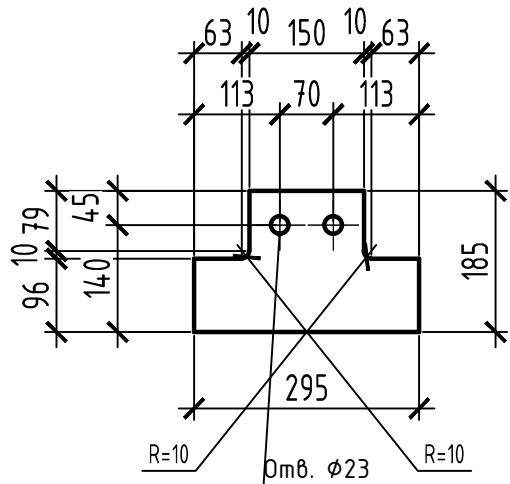

поз.24 (M1:10) 96 шт.
502006941C2459

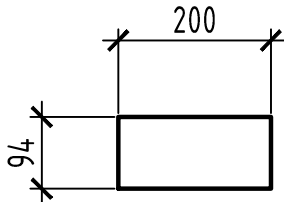


поз.32 (M1:10) 28 шт.
12070063001C2459

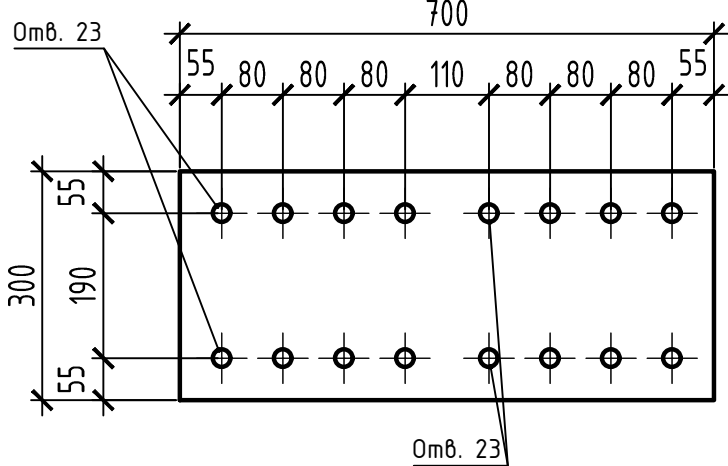

СПЕЦИФИКАЦИЯ							
№ детали	Кол-во шт.	Сечение	Длина мм	Вес, кг		Марка стали	Примечание
				Одной детали	Всех шт.		
22	158	† 12x140x547	547	7.21	1139.79	C245	
23	112	† 12x120x120	120	1.36	151.93	C245	
24	96	† 5x94x200	200	0.74	70.84	C245	
25	56	† 14x195x400	400	8.57	480.04	C245	
26	56	† 12x110x700	700	7.25	406.19	C245	
27	48	† 12x200x410	410	7.72	370.77	C245	
28	32	† 12x185x295	295	5.14	164.51	C245	
30	28	† 14x196x400	400	8.62	241.25	C245	
31	28	† 14x400x970	970	42.64	1193.95	C245	
32	28	† 12x300x700	700	19.78	553.9	C245	
33	28	† 12x400x700	700	26.38	738.53	C245	
34	16	† 12x140x268	268	3.53	56.44	C245	
35	14	† 30x200x260	260	12.25	171.44	C245	
36	14	† 30x720x970	970	164.47	2302.62	C245	
37	14	† 20x300x1260	1260	59.35	830.84	C245	
38	8	† 12x185x295	295	5.14	41.13	C245	
39	8	† 12x260x336	336	8.23	65.83	C245	
Итого:				8980.02			

						№929-26-КМД (05-09/24-КМ). "Реконструкция здания главного корпуса с инвентарным номером 110/С-97826 производственного филиала ОАО "Савушкин продукт" г.Барановичи, ул. 50 лет БССР, 51/1"		
						Нет,Опорная плита,Пластина,Пластина		
Изм.	Кол.уч	Лист	Идок.	Подпись	Дата	ета,Пластина усиления,Пластина-накладка,Ребро жесткости,Торцевая пластина	Стадия	Масса
Гл.Инженер					18.06.2026	22,23,24,25,26,27,28,30,31,32,33,34,35,36,37,38,39		
Нач. отдела					18.06.2026			
Н.Контр.					18.06.2026		Лист 02	Листов
					18.06.2026		000 "АльденаГрупп"	
Разработал					18.06.2026			

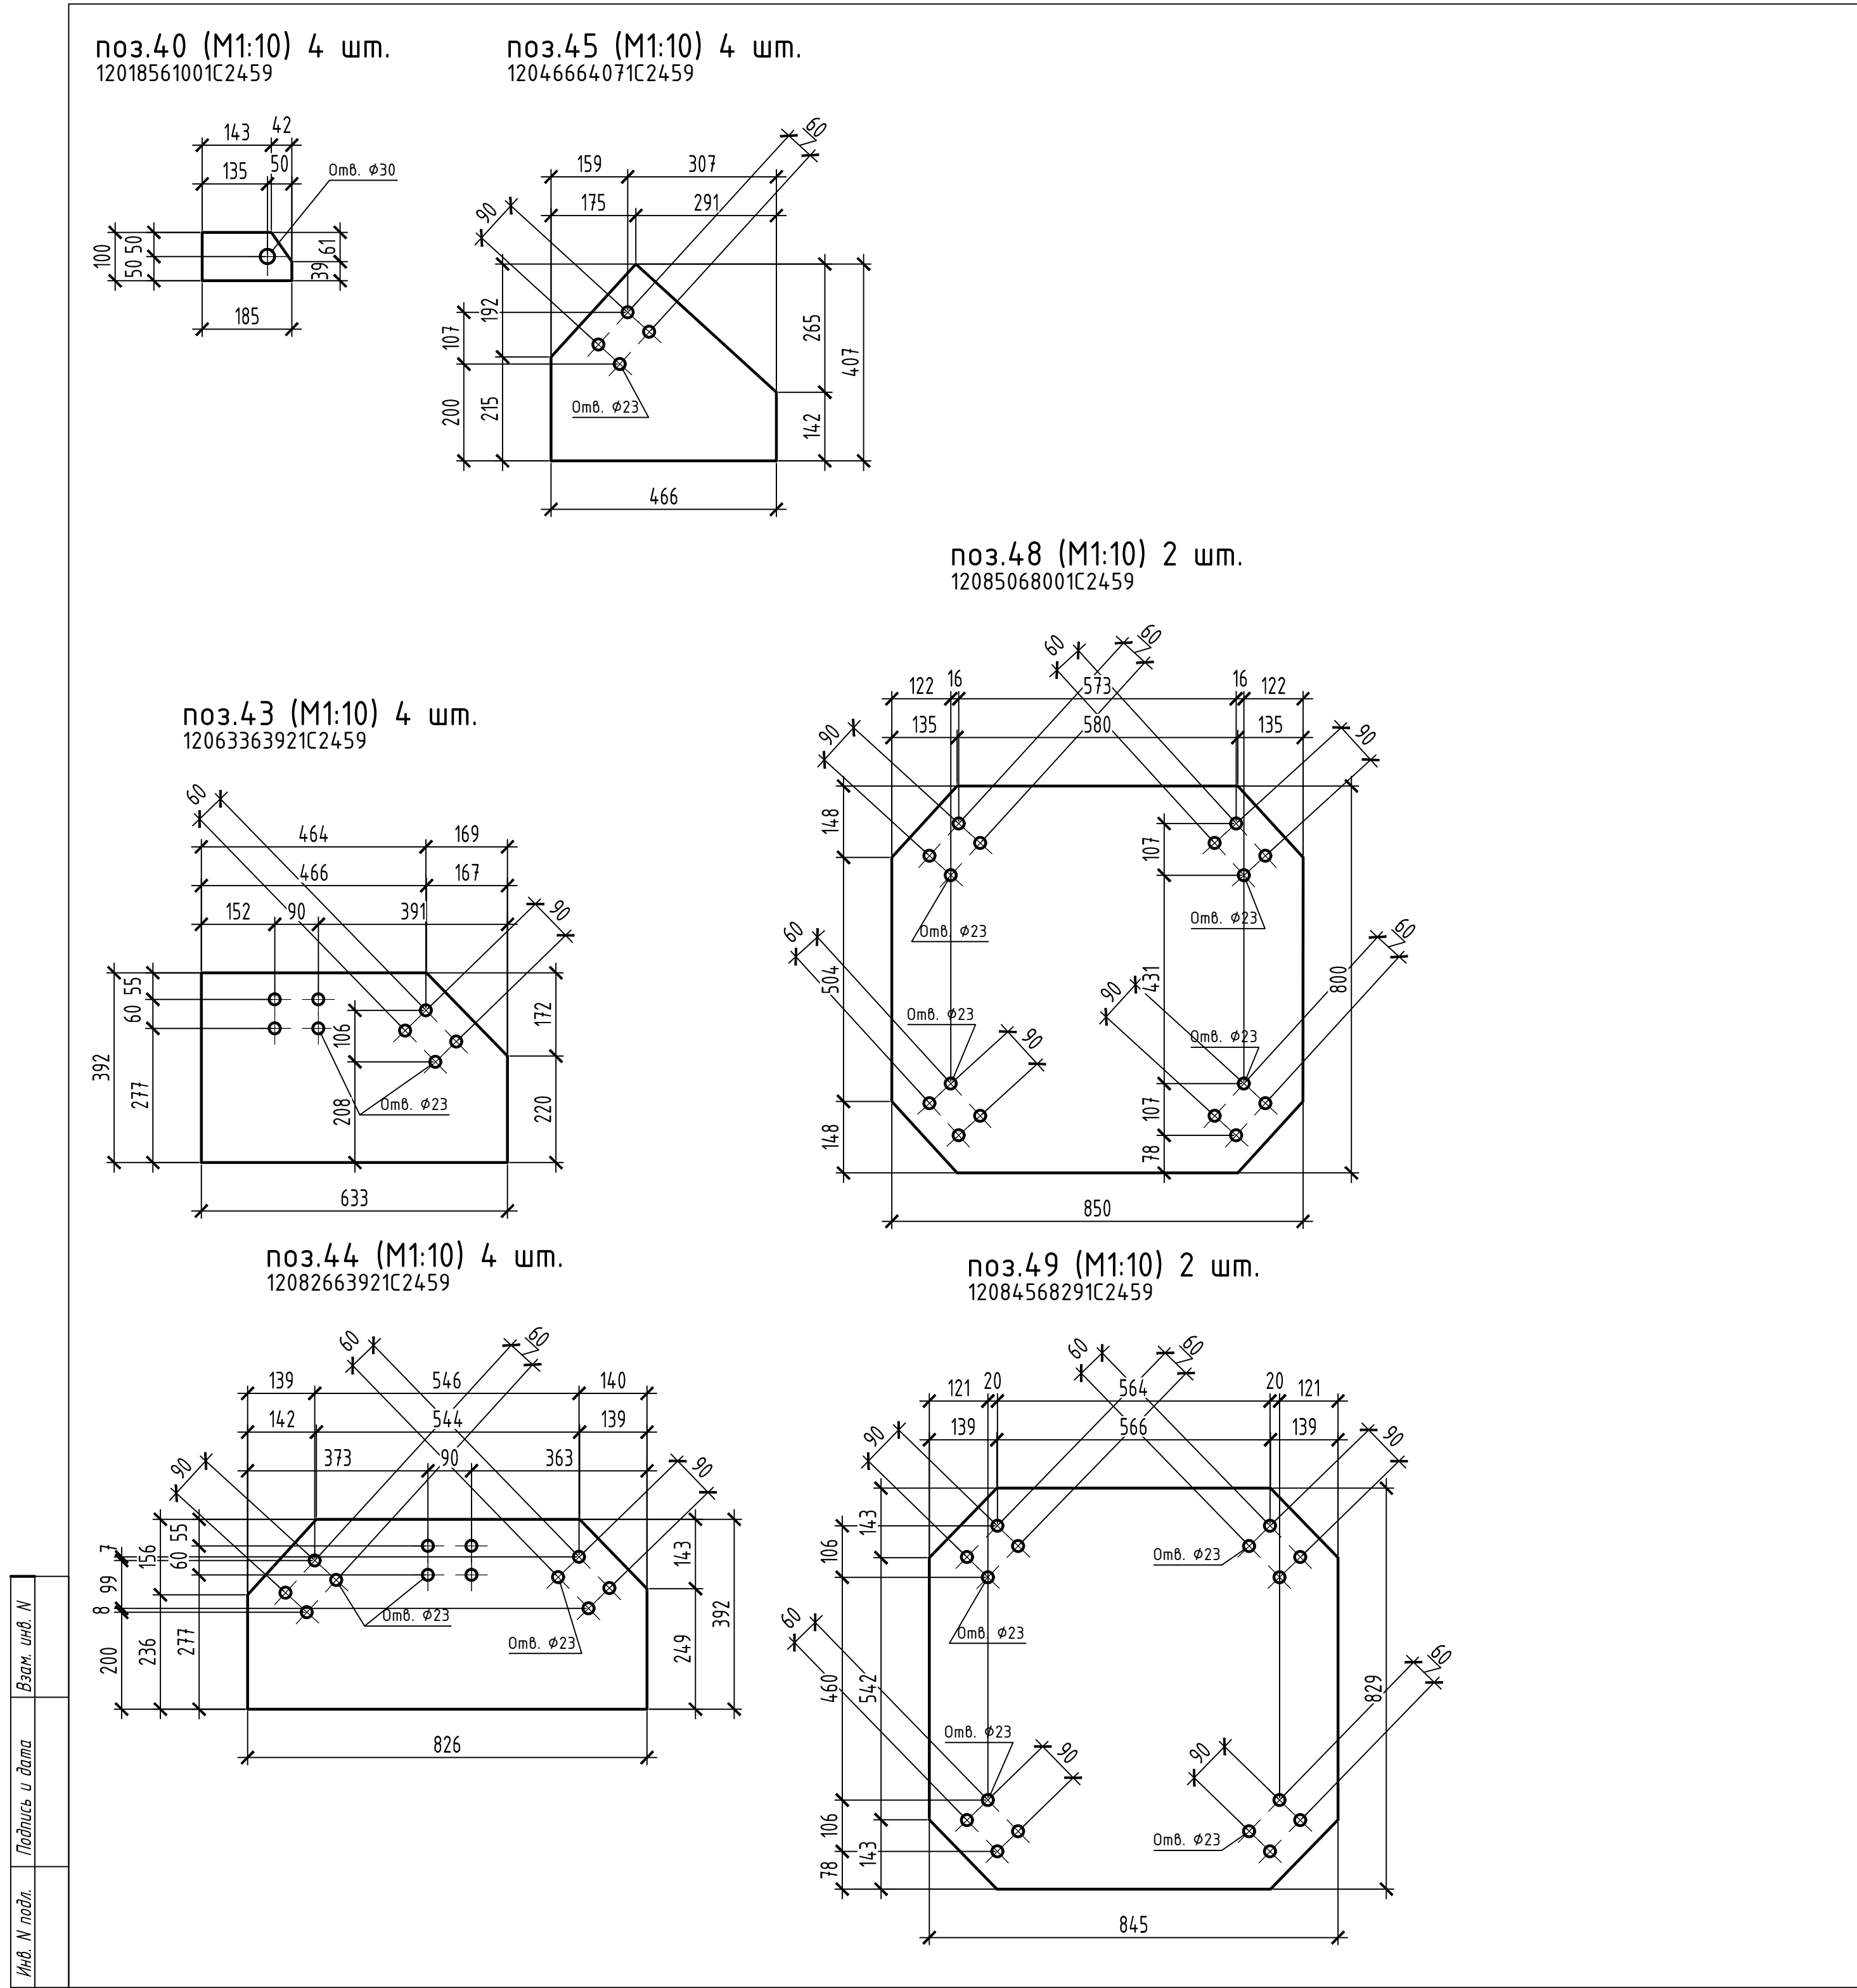

СПЕЦИФИКАЦИЯ							
№ детали	Кол-во шт.	Сечение	Длина мм	Вес, кг		Марка стали	Примечание
				Одной детали	Всех шт.		
40	8	† 12х100х185	185	1.74	13.94	С245	
43	4	† 12х392х633	633	23.39	93.57	С245	
44	4	† 12х392х826	826	30.52	122.09	С245	
45	4	† 12х407х466	466	17.86	71.44	С245	
48	2	† 12х800х850	850	64.06	128.11	С245	
49	2	† 12х829х845	845	65.94	131.87	С245	
Итого:				561.03			

						Техническая эксплуатация изолированного помещения №1 с инвентарным номером 100/D-141367? расположенного по адресу : г.Брест, ул. Спокойная 1-1"				
Изм.	Колуч	Лист	Ндок.	Подпись	Дата	Нет,Узловая фасонка		Стадия	Масса	Масштаб
Гл.Инженер		Михнюк Д.В.			18.06.2026					1:10
Нач. отдела		Иванюк В.С.			18.06.2026					
					18.06.2026			Лист 03	Листов	
Н.Контр.		Иванюк В.С.			18.06.2026	ООО "АльденаГрупп"				
					18.06.2026					
Разработал		Иванюк В.С.			18.06.2026					