
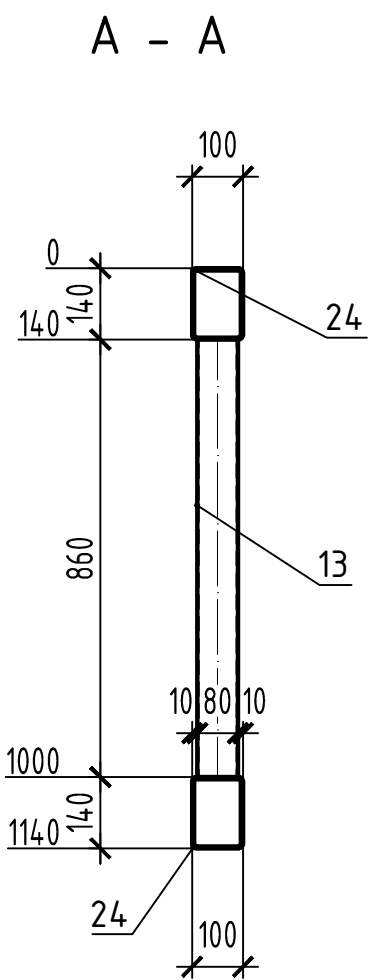
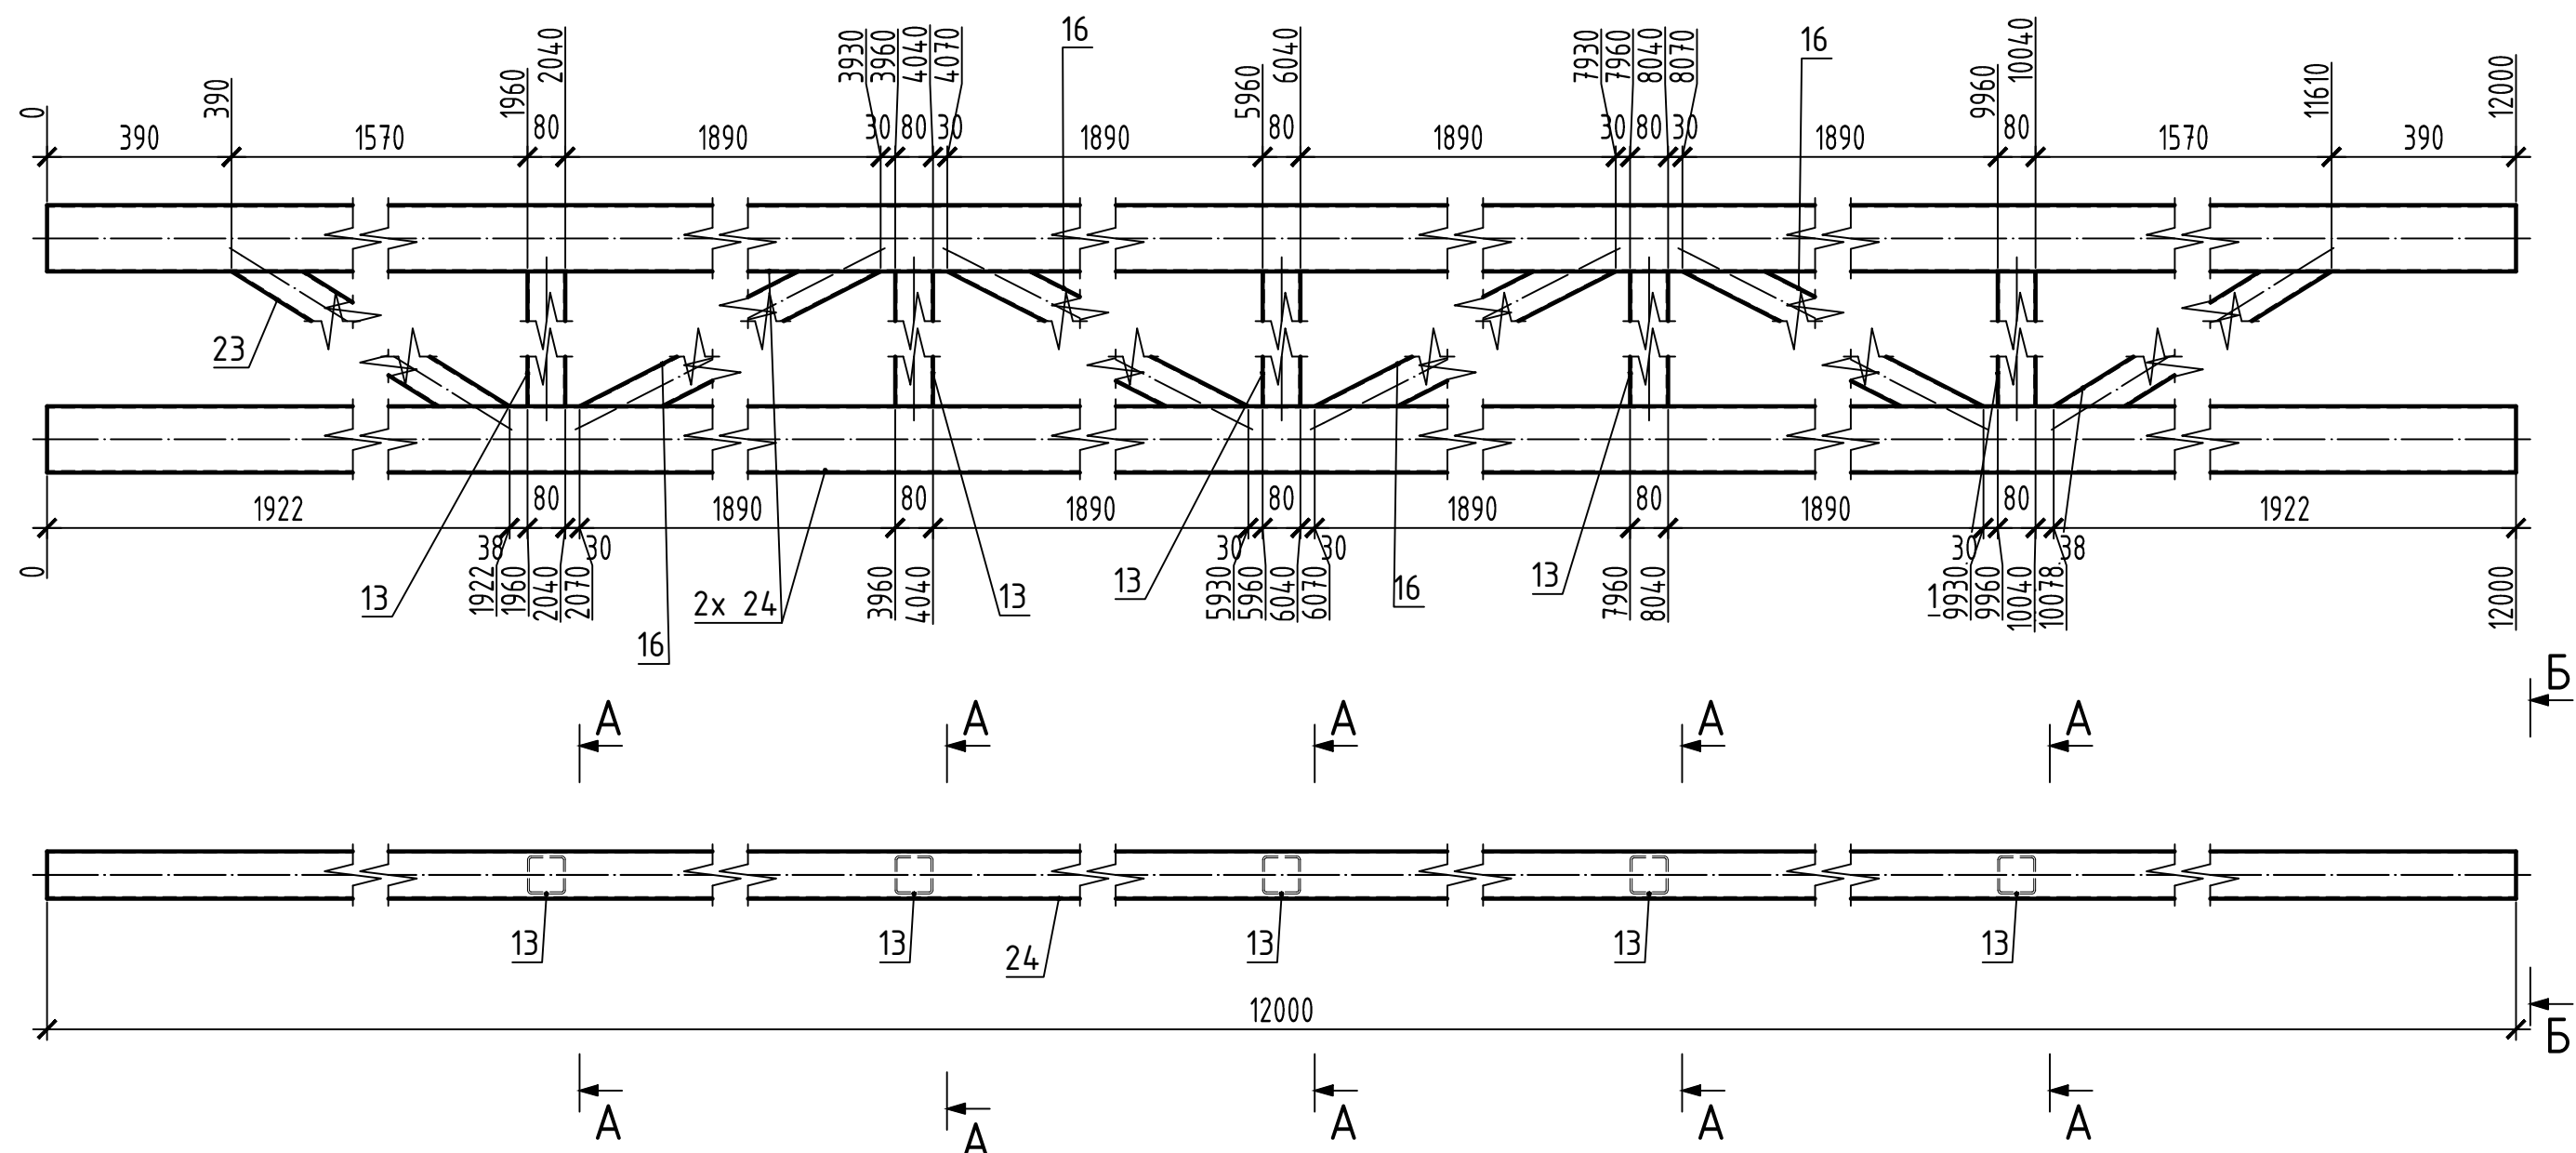


Спецификация на отправочный элемент										
Марка	Поз.	Кол-во, шт.		Сечение	Длина, мм	Масса, кг			Марка стали	Примечание
		т	н			шт.	общ.	эле.		
ФМ1	23	2		Гн. 80х4	1755	16.18	32.36	494.41	С245	
	16	4		Гн. 80х4	2047	18.88	75.51		С245	
	13	5		Гн. 80х4	860	7.93	39.65		С245	
	24	2		Гн. 140х100х4	12000	171	342		С245	
			На сварные швы 1%						4.9	

Требуется изготовить			
Упр. марка	Кол-во, шт.	Масса, кг	
		шт.	общ.
ФМ1	2	494.41	988.82
		Итого: 988.82	

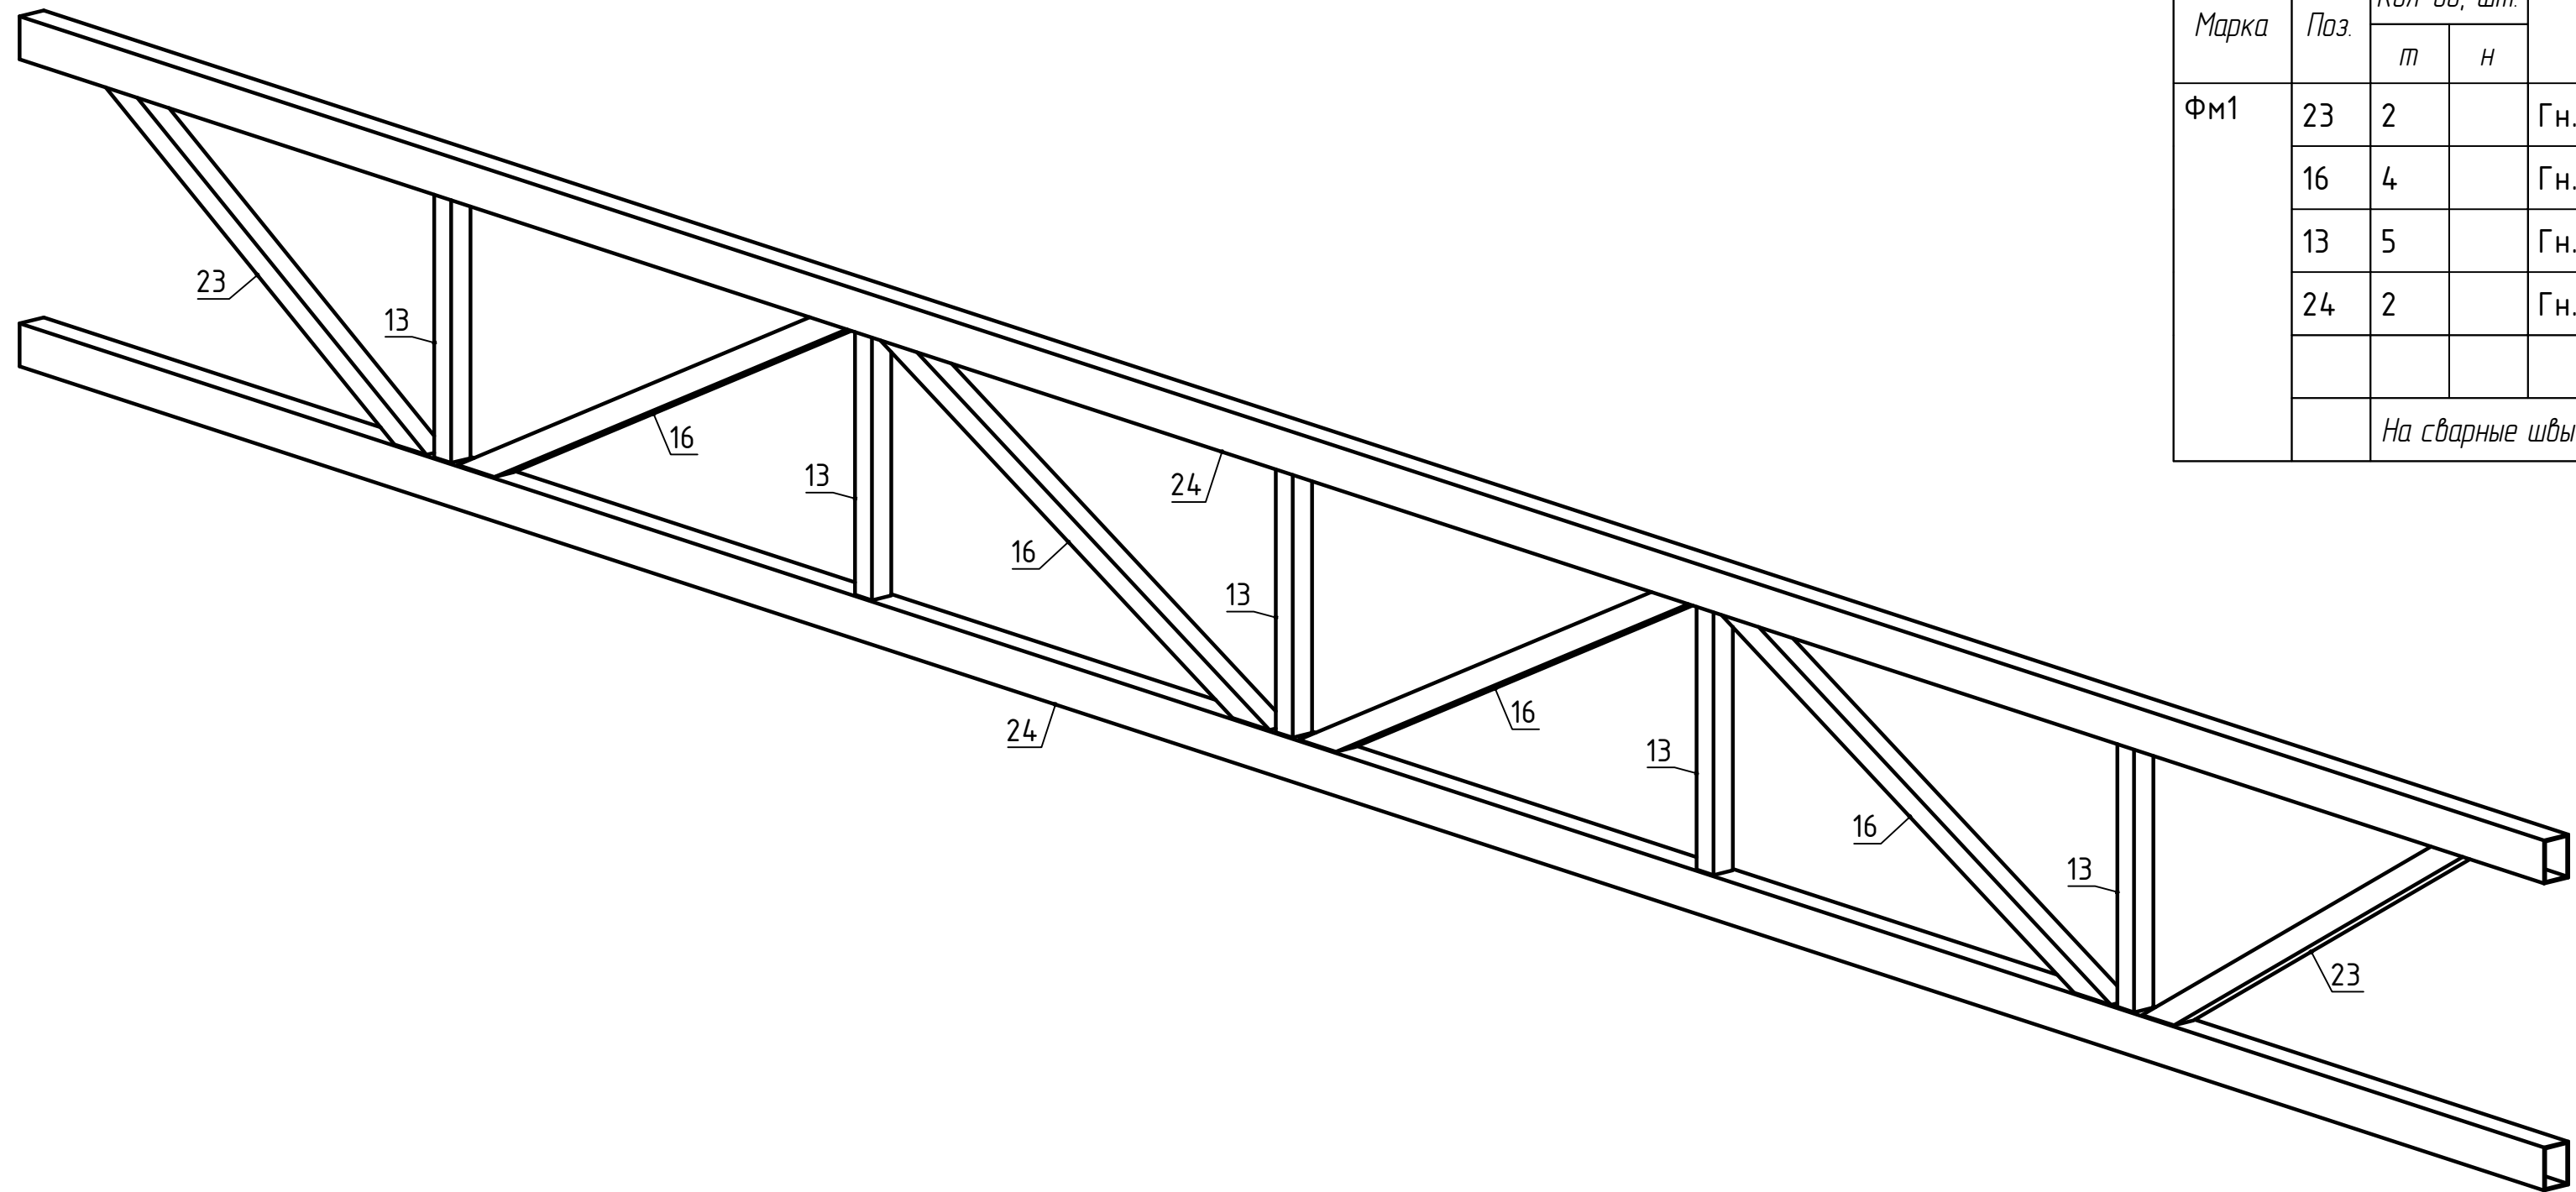

						927-26. Устройство площадок под рамы оборудования на чердаке компрессорной в осях Г/1-Д/1 - 1/1-5/1
Изм.	Кол-во	Лист	Подк.	Подпись	Дата	Ферма
Гл.Инженер		Михнюк Д.В.			08.06.2026	ФМ1
Нач. отдела		Иванюк В.С.			08.06.2026	
					08.06.2026	
Н.Контр.		Иванюк В.С.			08.06.2026	Лист 06
Разработал		Иванюк В.С.			08.06.2026	Листов
						ООО "АльдегаГрупп"

Инв. N подл.	Подпись и дата	Взам. инв. N