
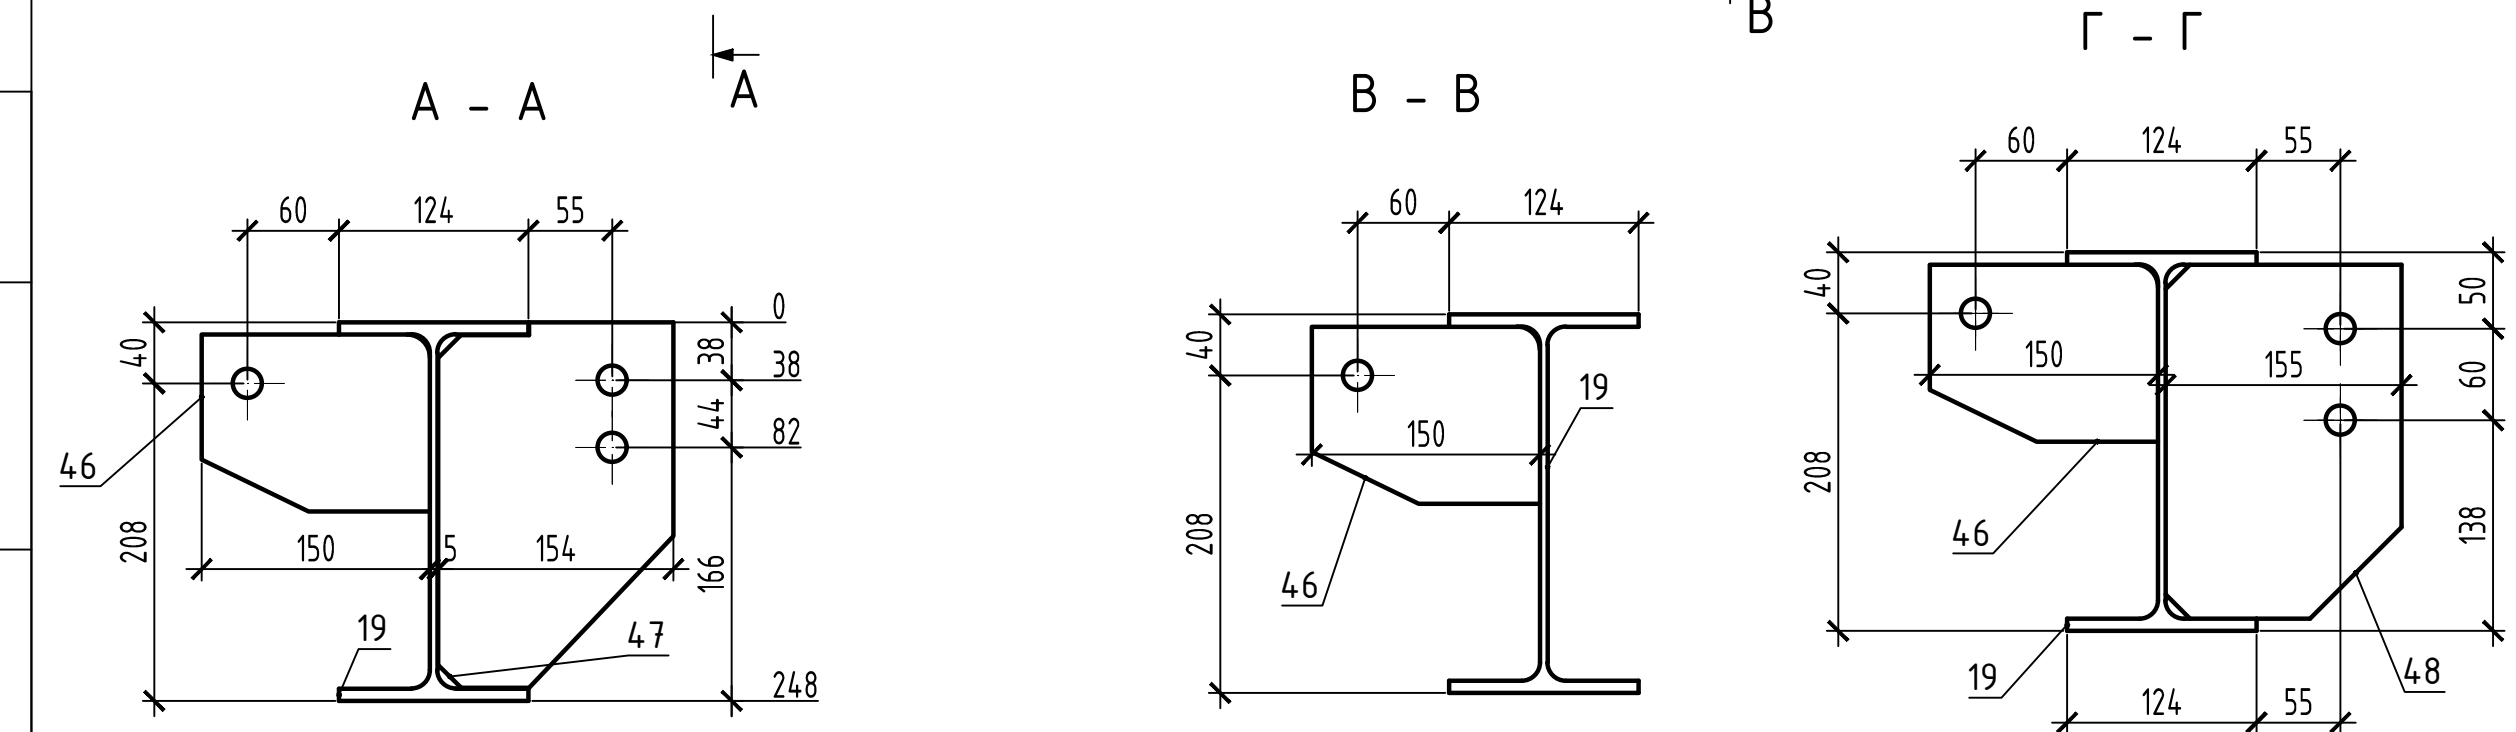
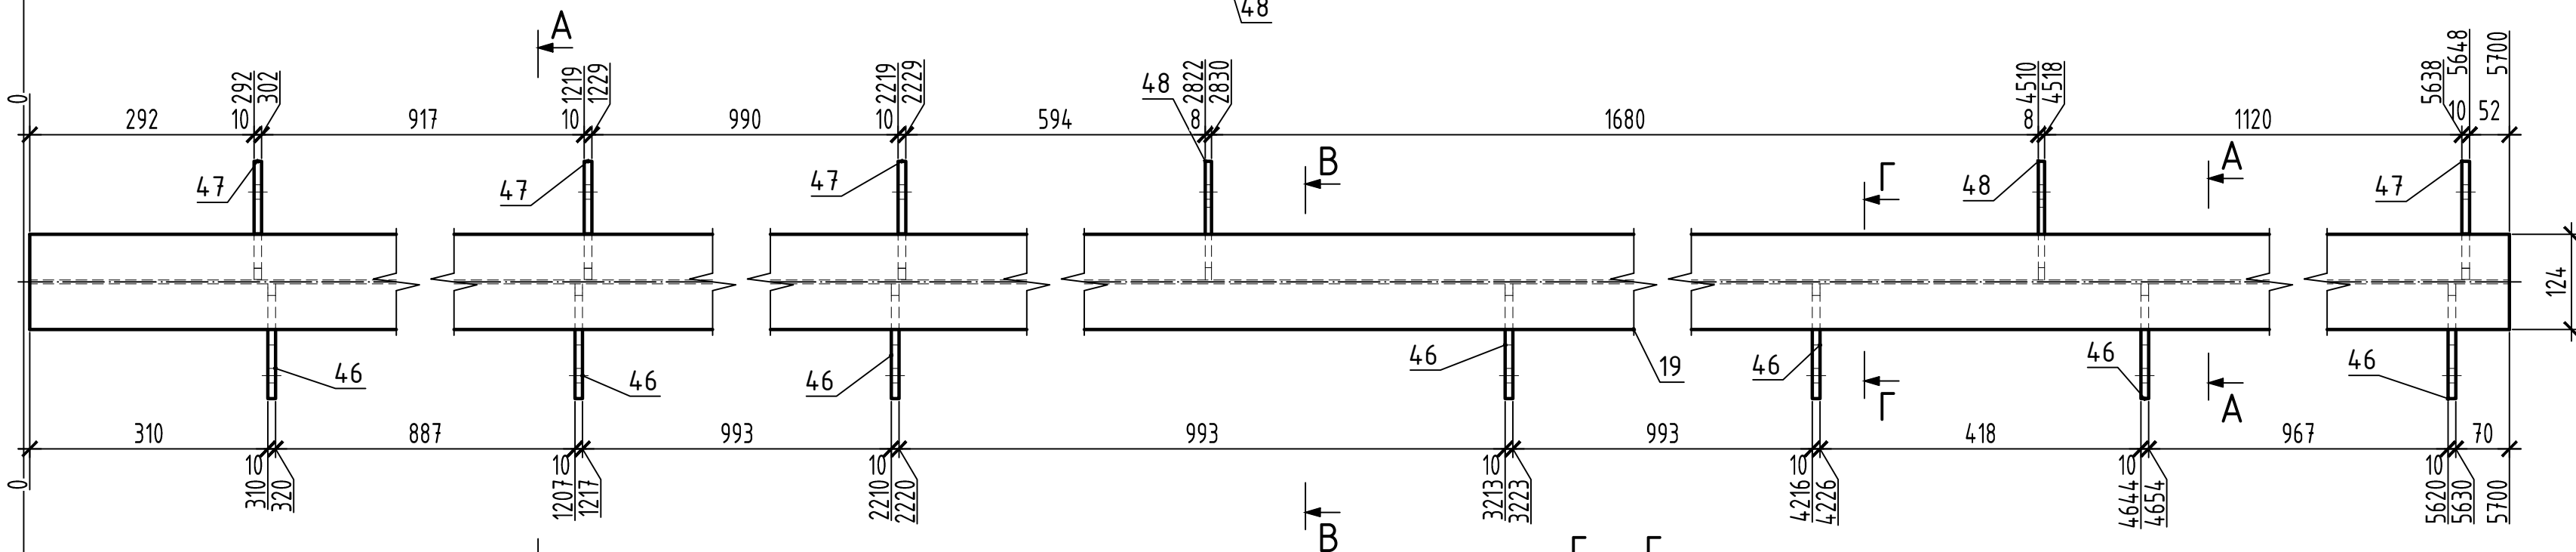


Марка Б1-1 (1 шт.)

Спецификация на отправочный элемент									
Марка	Поз.	Кол-во, шт.		Сечение	Длина, мм	Масса, кг			Примечание
		т	н			шт.	общ.	элемент	
Б1-1	19	1		12551	5700	146.49	146.49	173.82	С245
	48	2		† 8х154х232	232	2.25	4.5		С245
	46	7		† 10х116х150	150	1.36	9.53		С245
	47	4		† 10х154х239	239	2.9	11.58		С245
На сварные швы 1%							1.72		

Требуется изготовить			
Испр. марка	Кол-во, шт.	Масса, кг	
		шт.	общ.
Б1-1	1	173.82	173.82
Итого:		173.82	

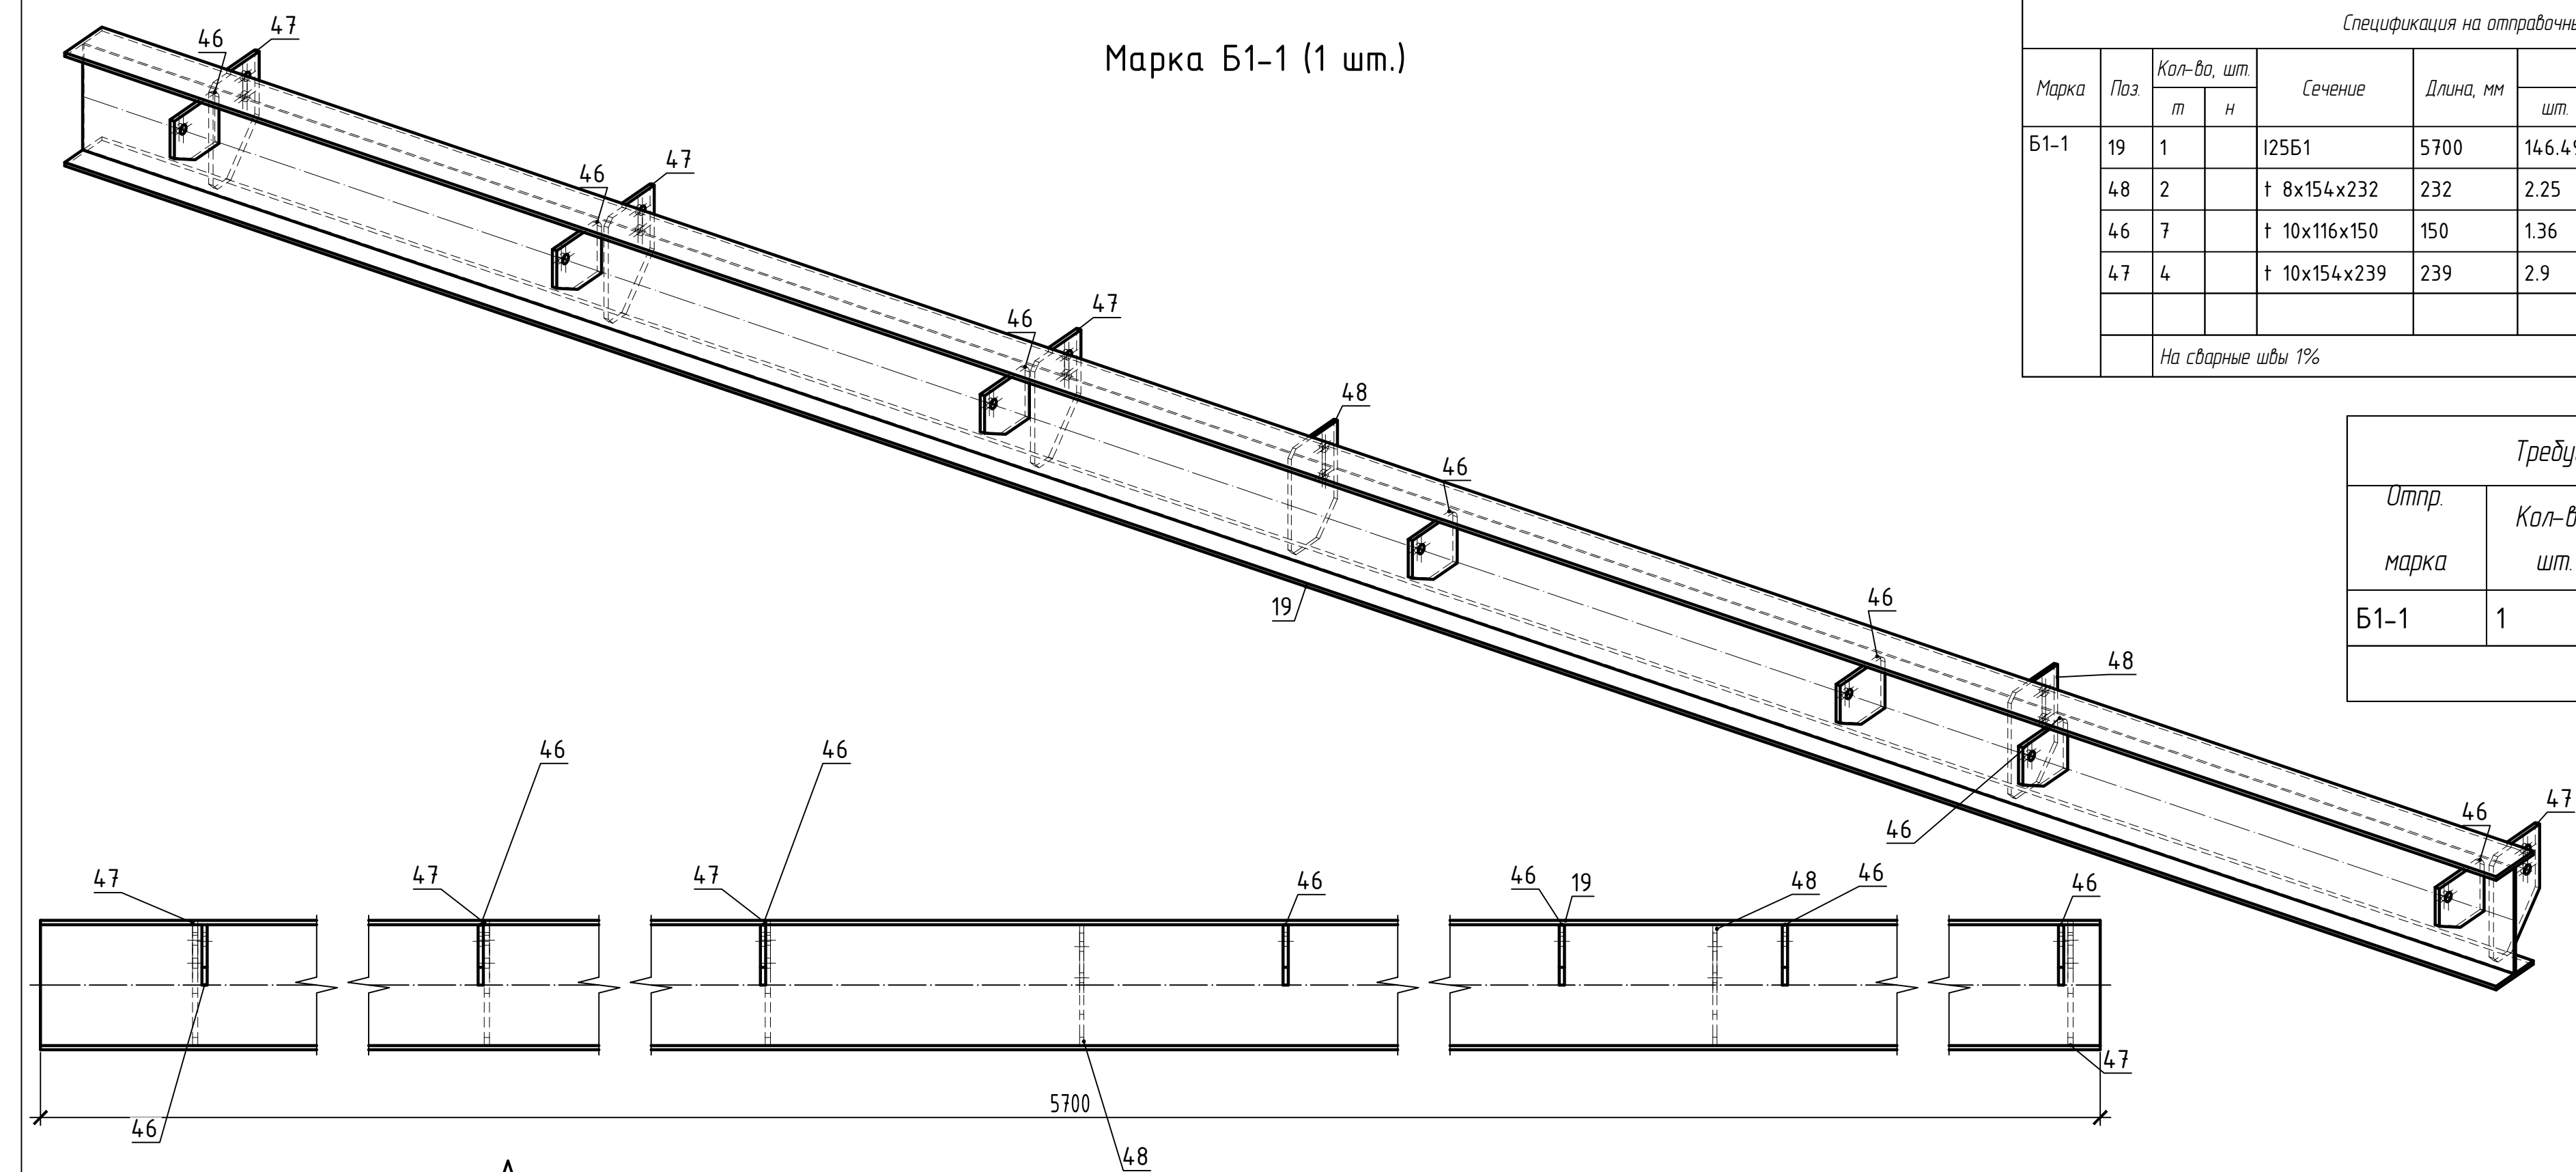

						927-26. Устройство площадок под рамы оборудования на чердаке компрессорной в осях Г/1-Д/1 - 1/1-5/1			
Изм.	Колуч	Лист	Издок.	Подпись	Дата	Балка Б1-1	Стадия	Масса	Масштаб
Гл.Инженер		Мухнюк Д.В.			08.06.2026				1:10, 1:5, 1:7.5
Нач. отдела		Иванюк В.С.			08.06.2026				
					08.06.2026		Лист 07	Листов	
Н.Контр.		Иванюк В.С.			08.06.2026		ООО "АльдегаГрупп"		
					08.06.2026				
Разработал		Иванюк В.С.			08.06.2026				