

Б - Б


Спецификация на отправочный элемент

Марка	Поз.	Кол-во, шт.		Сечение	Длина, мм	Масса, кг			Марка стали	Примечание
		т	н			шт	общ	эле		
К-3	7	1		160Ш2	6000	1024.2	1024.2	14.01.35	С245	
	34	2		† 12х140х268	268	3.53	7.06		С245	
	22	4		† 12х140х547	547	7.21	28.86		С245	
	39	1		† 12х260х336	336	8.23	8.23		С245	
	45	1		† 12х407х466	466	17.86	17.86		С245	
	25	4		† 14х195х400	400	8.57	34.29		С245	
	30	2		† 14х196х400	400	8.62	17.23		С245	
	31	2		† 14х400х970	970	42.64	85.28		С245	
	36	1		† 30х720х970	970	164.47	164.47		С245	
			На сварные швы 1%				13.87			


A - A

Требуется изготовить			
Тип марка	Кол-во, шт.	Масса, кг	
		шт.	общ.
К-3	2	1401.35	2802.7
		Итого: 2802.7	



						№929-26-КМД (05-09/24-КМ). "Реконструкция здания главного корпуса с инвентарным номером 110/С-97826 производственного филиала ОАО "Савушкин продукт" г.Барановичи, ул. 50 лет БССР, 51/1"			
Изм.	Кол.уч	Лист	Идок.	Подпись	Дата	Нет	Стадия	Масса	Масштаб
Гл.Инженер	Мухомов	Д.В.			18.06.2026				1:10, 1:15, 1:20, 1:7.
Нач. отдела	Иванюк	В.С.			18.06.2026	К-3			
					18.06.2026		Лист 06	Листов	
Н.Контр.	Иванюк	В.С.			18.06.2026		ООО "АльдегаГрупп"		
					18.06.2026				
Разработал	Иванюк	В.С.			18.06.2026				

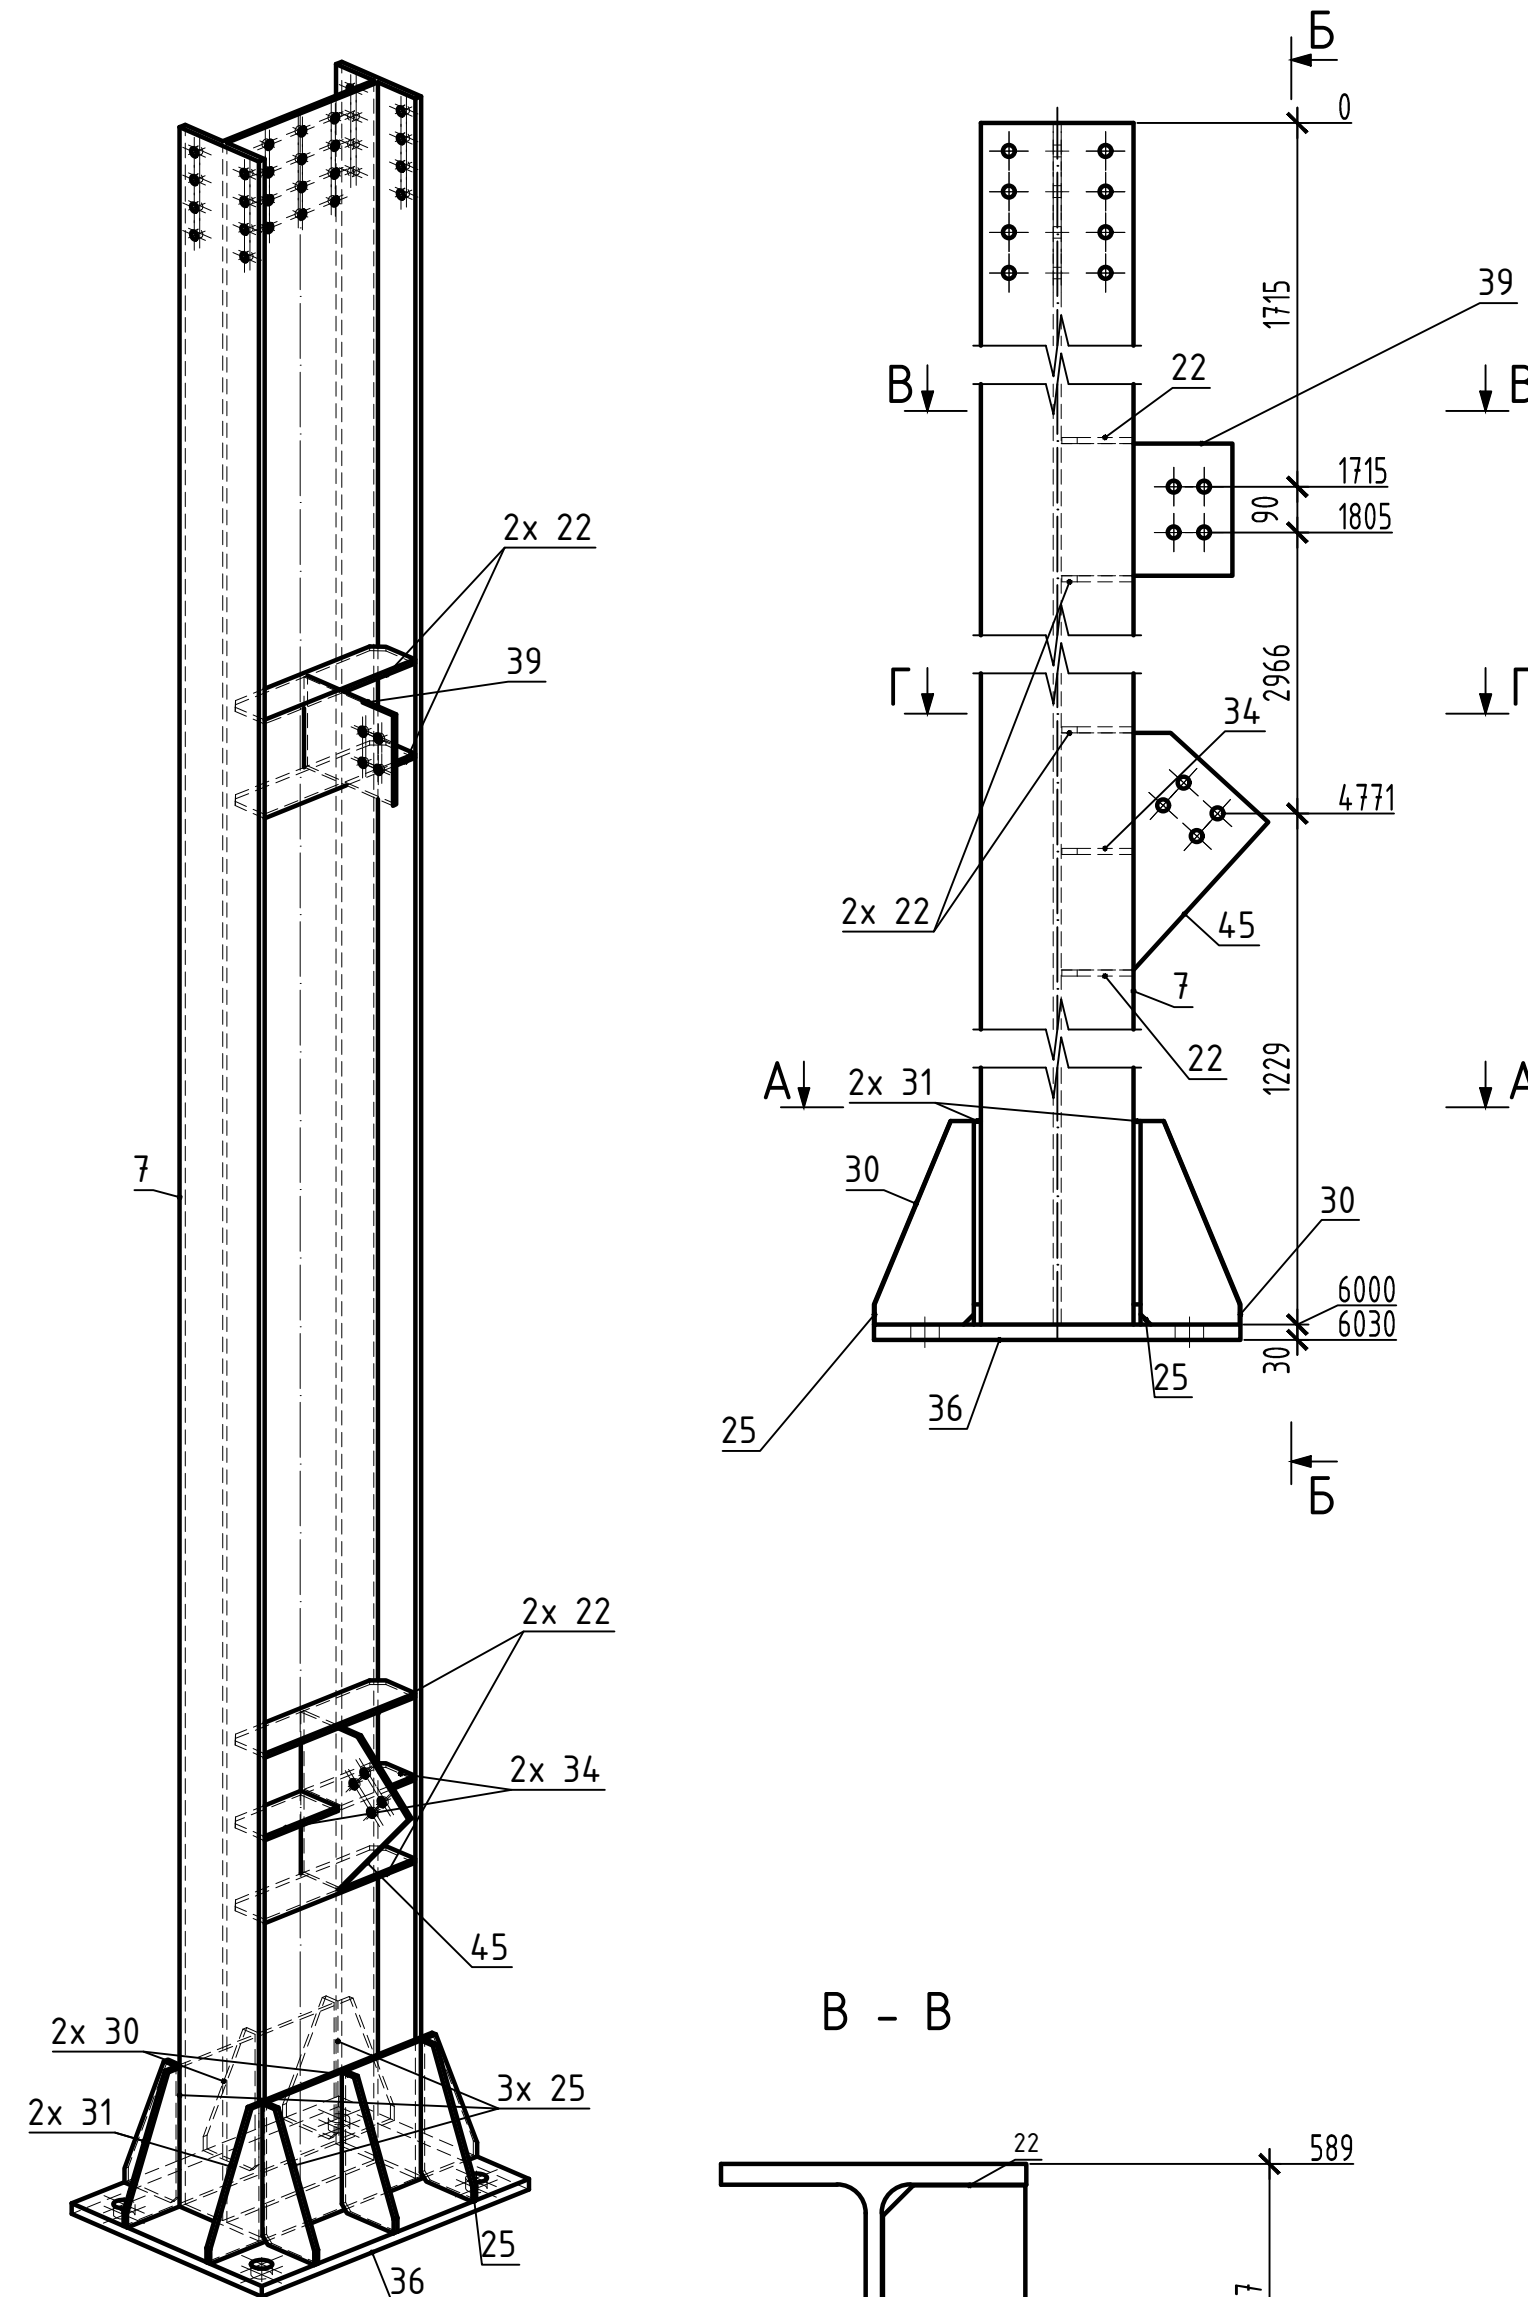

B - B

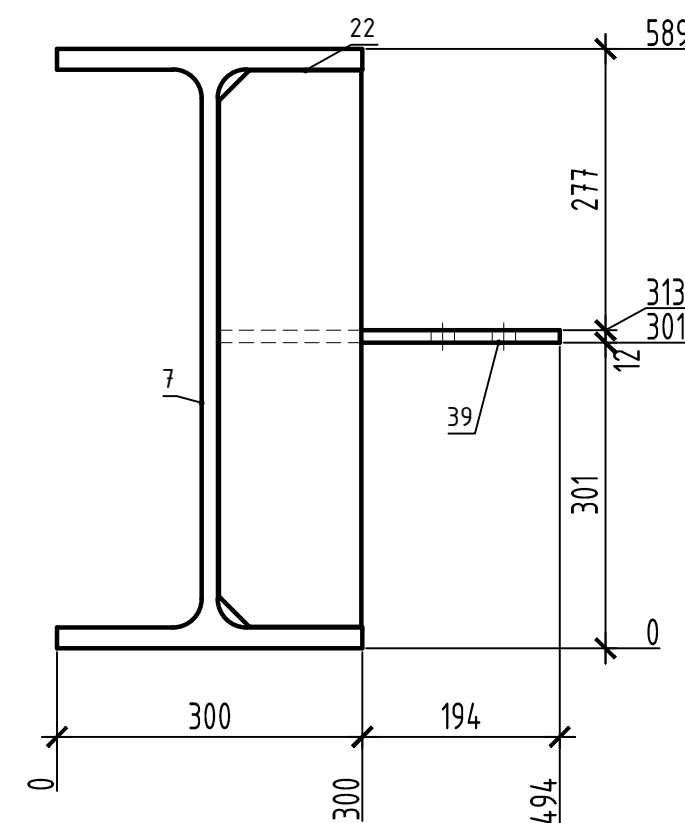

┌ ─ ┌

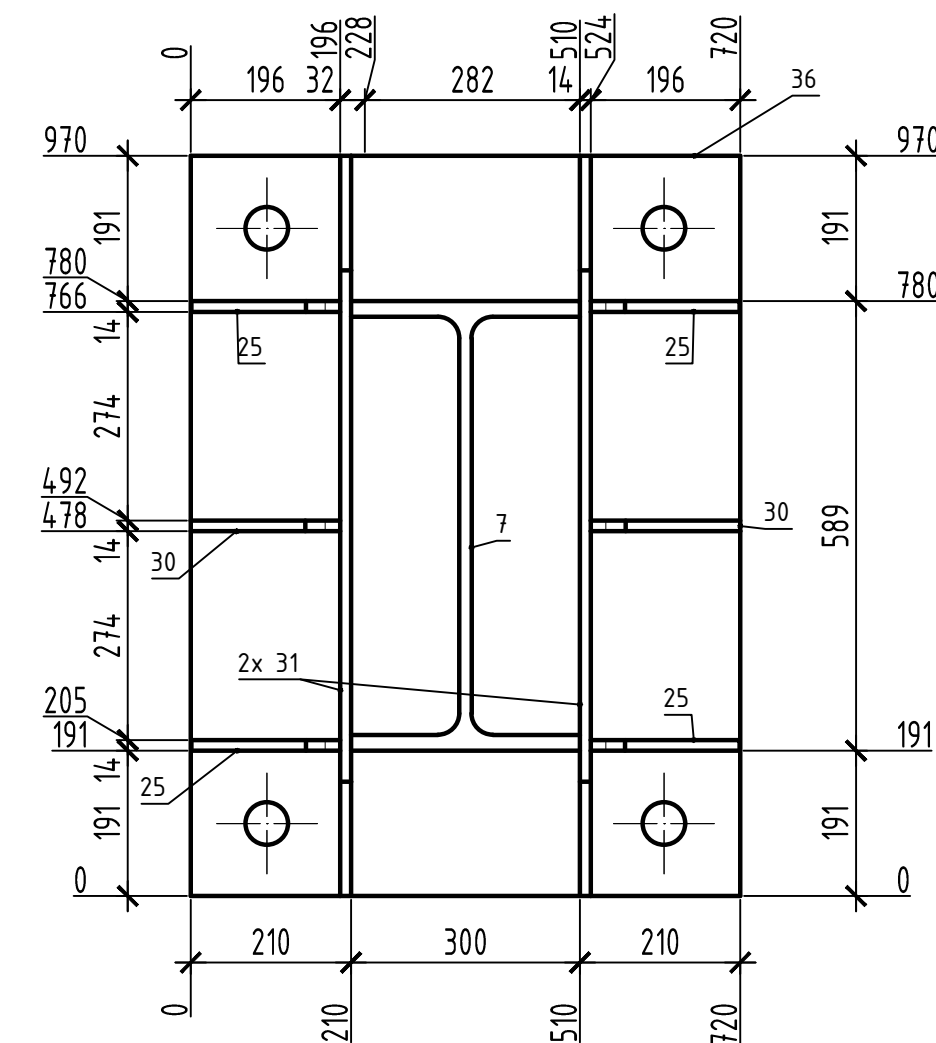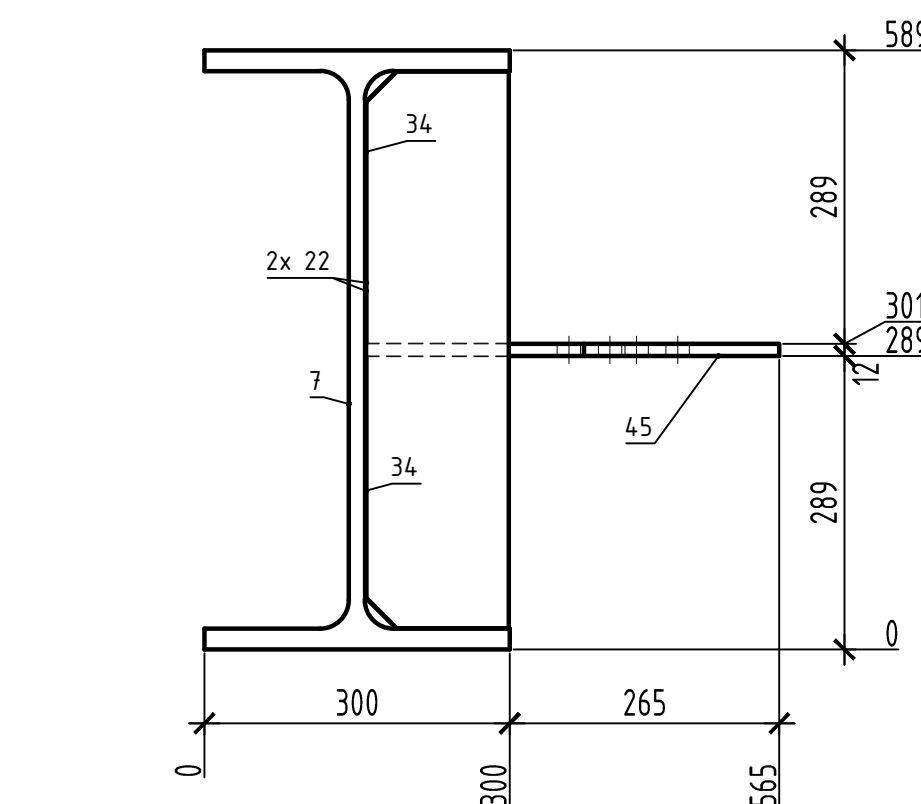

Инв. N подл.	Подпись и дата	Взам. инв. N