

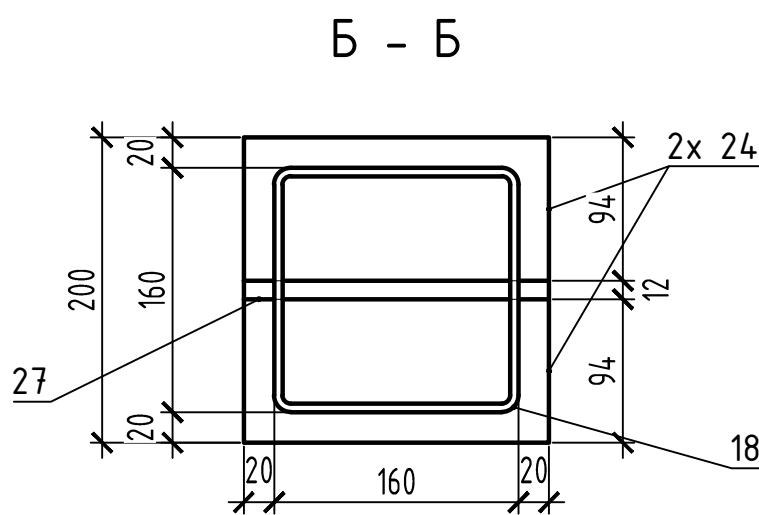
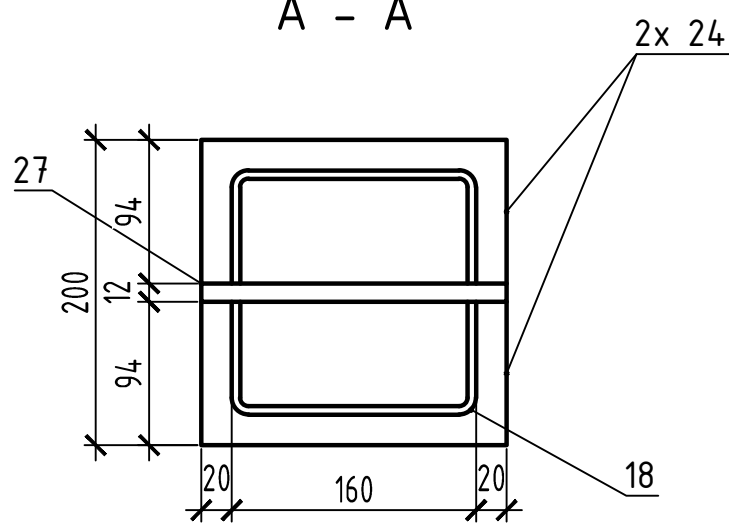
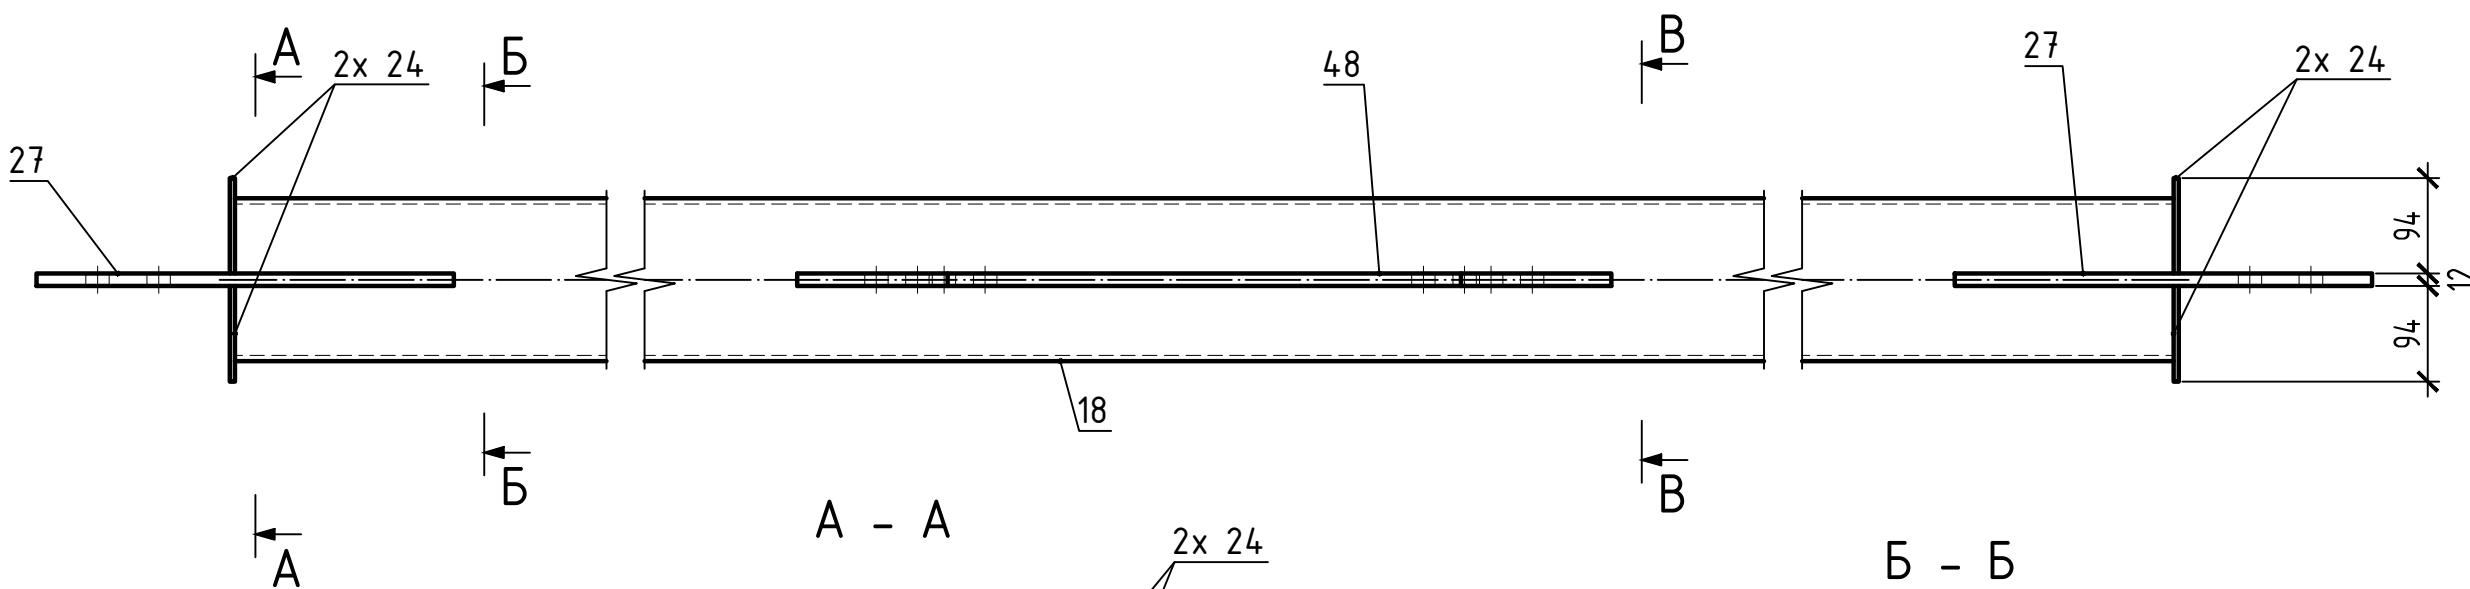
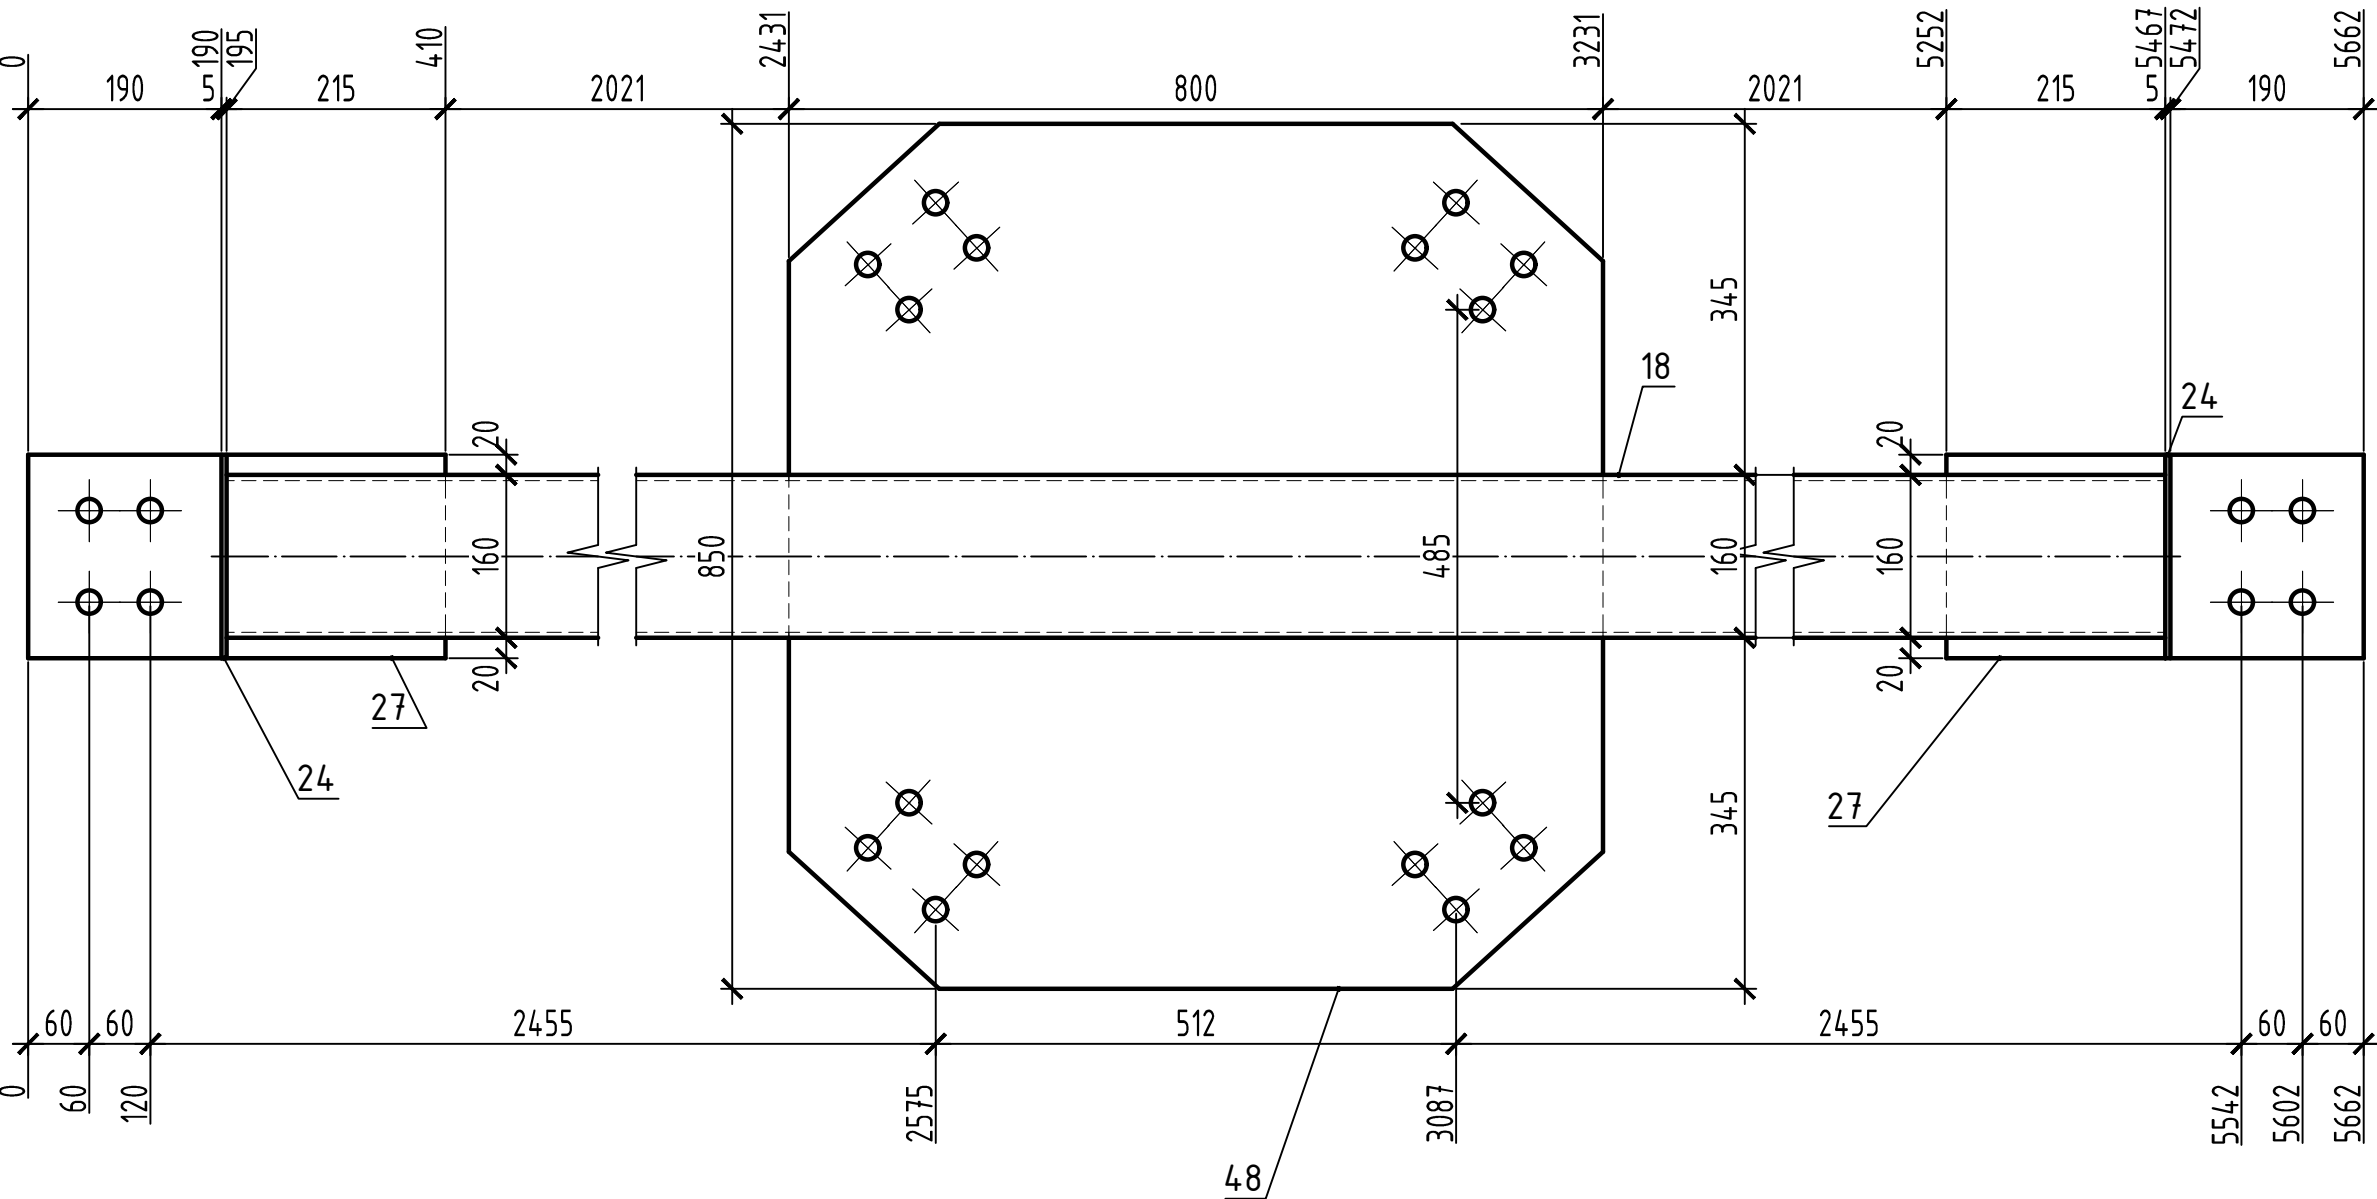


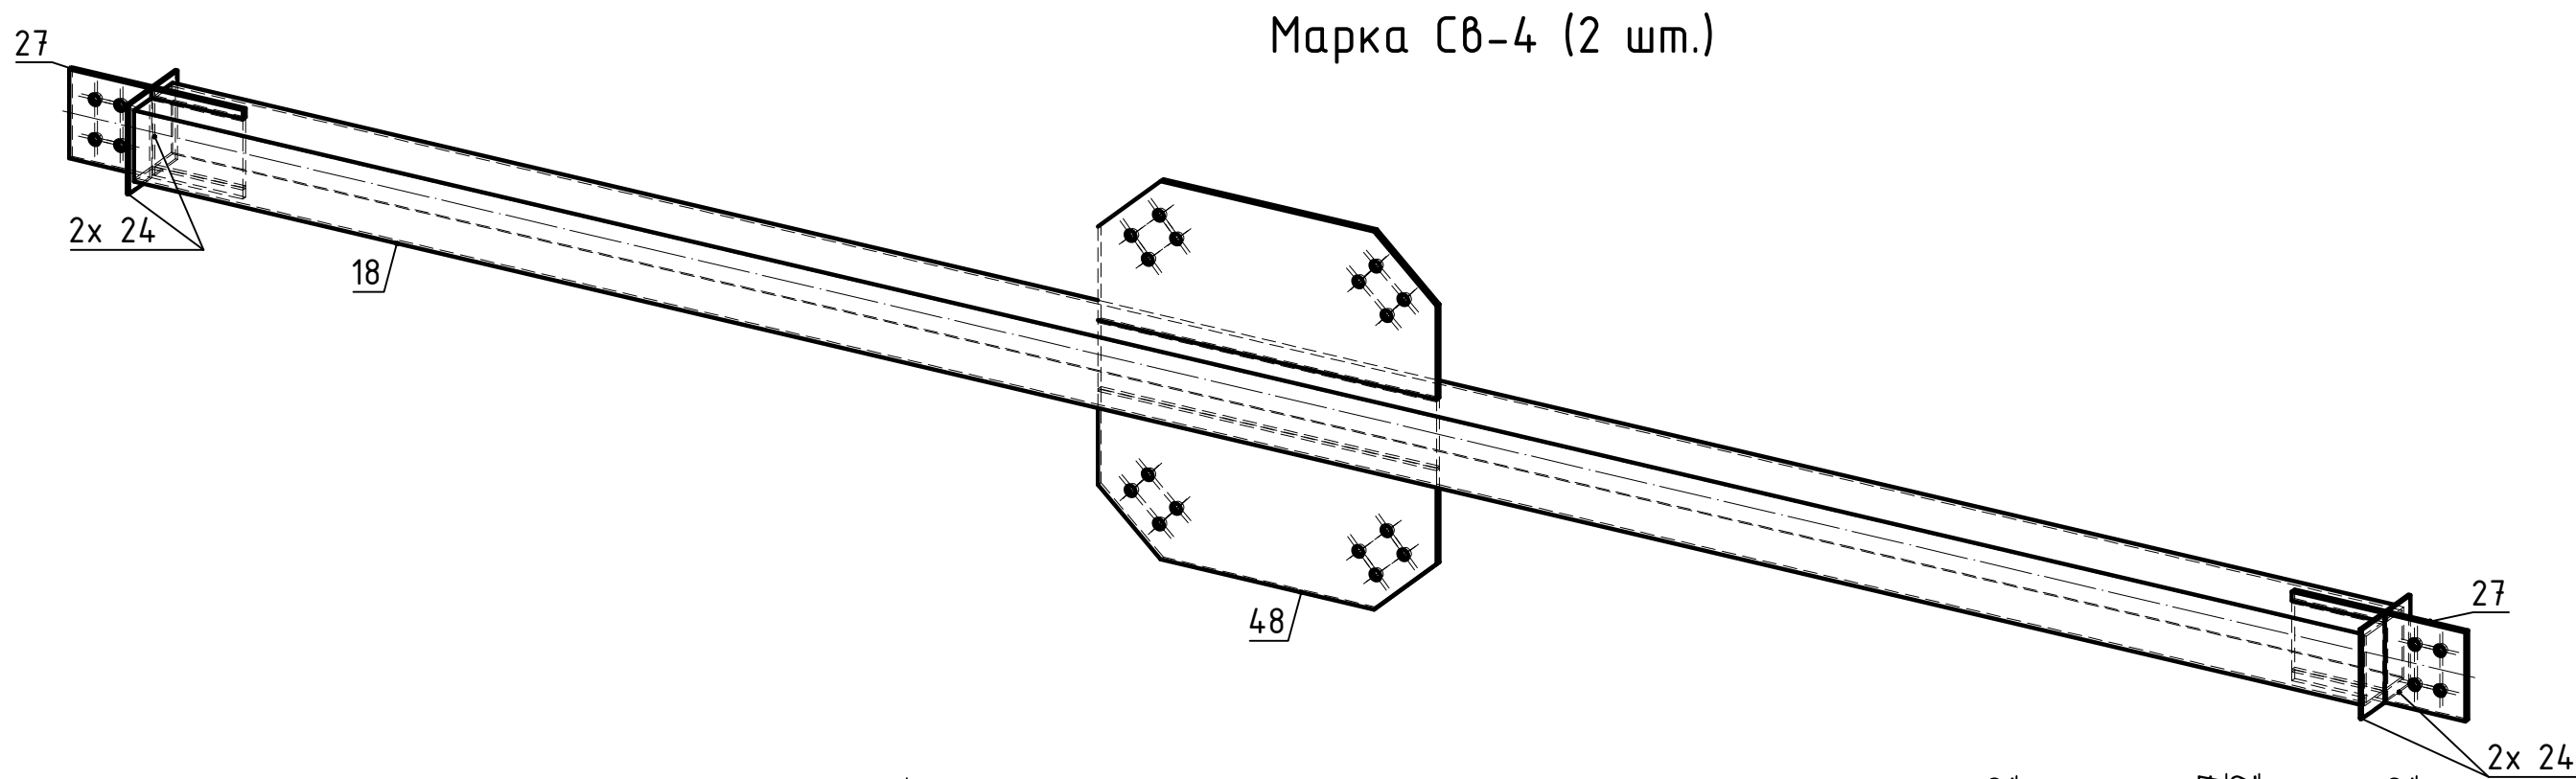

Спецификация на отправочный элемент									
Марка	Поз.	Кол-во, шт.		Сечение	Длина, мм	Масса, кг			Примечание
		т	н			шт.	общ.	элемент	
Св-4	18	1		Гн. 160х5.5	5272	137.44	137.44		С245
	24	4		† 5х94х200	200	0.74	2.95		С245
	27	2		† 12х200х410	410	7.72	15.45		С245
	48	1		† 12х800х850	850	64.06	64.06		С245
	На сварные швы 1%						2.2	222.1	

Требуется изготовить			
Испр. марка	Кол-во, шт.	Масса, кг	
		шт.	общ.
Св-4	2	222.1	444.19
Итого: 444.19			

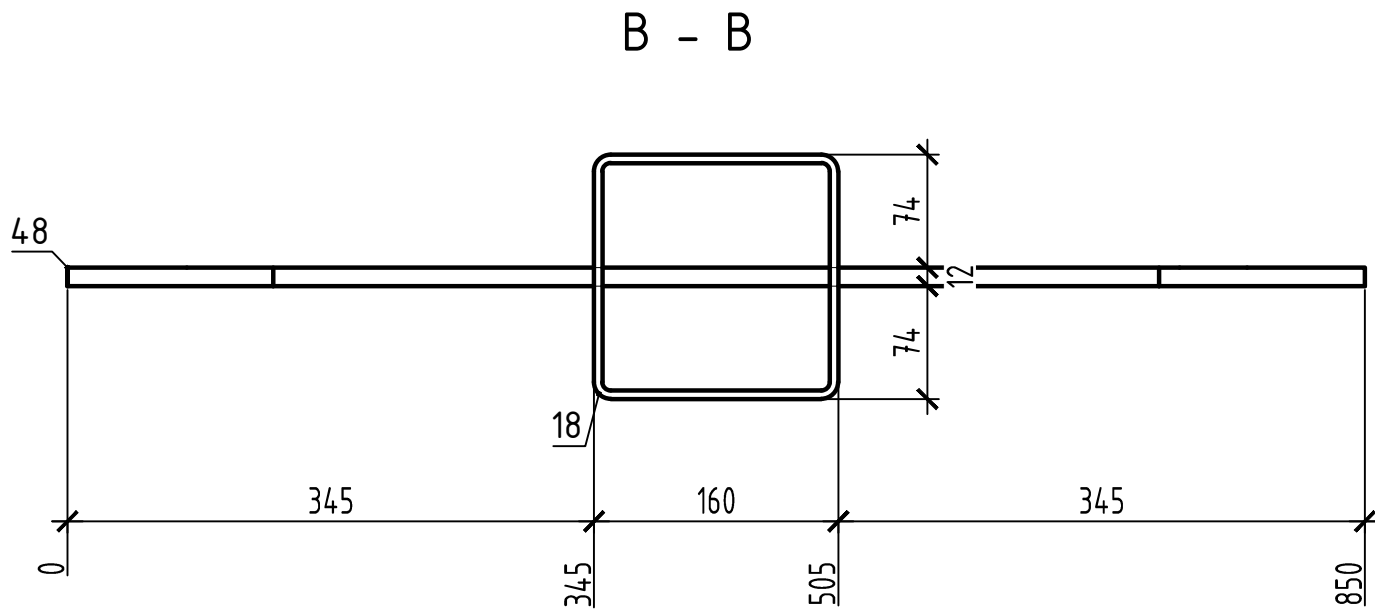

						№929-26-КМД (05-09/24-КМ). "Реконструкция здания главного корпуса с инвентарным номером 110/С-97826 производственного филиала ОАО "Савушкин продукт" г.Барановичи, ул. 50 лет БССР, 51/1"			
Изм.	Колуч	Лист	Идок.	Подпись	Дата	Нет СВ-4	Стадия	Масса	Масштаб
Гл.Инженер		Михнюк Д.В.			19.06.2026				1:15, 1:20, 1:5, 1:7.5
Нач. отдела		Иванюк В.С.			19.06.2026				
					19.06.2026		Лист 24	Листов	
Н.Контр.		Иванюк В.С.			19.06.2026		ООО "АльденаГрупп"		
					19.06.2026				
Разработал		Иванюк В.С.			19.06.2026				