
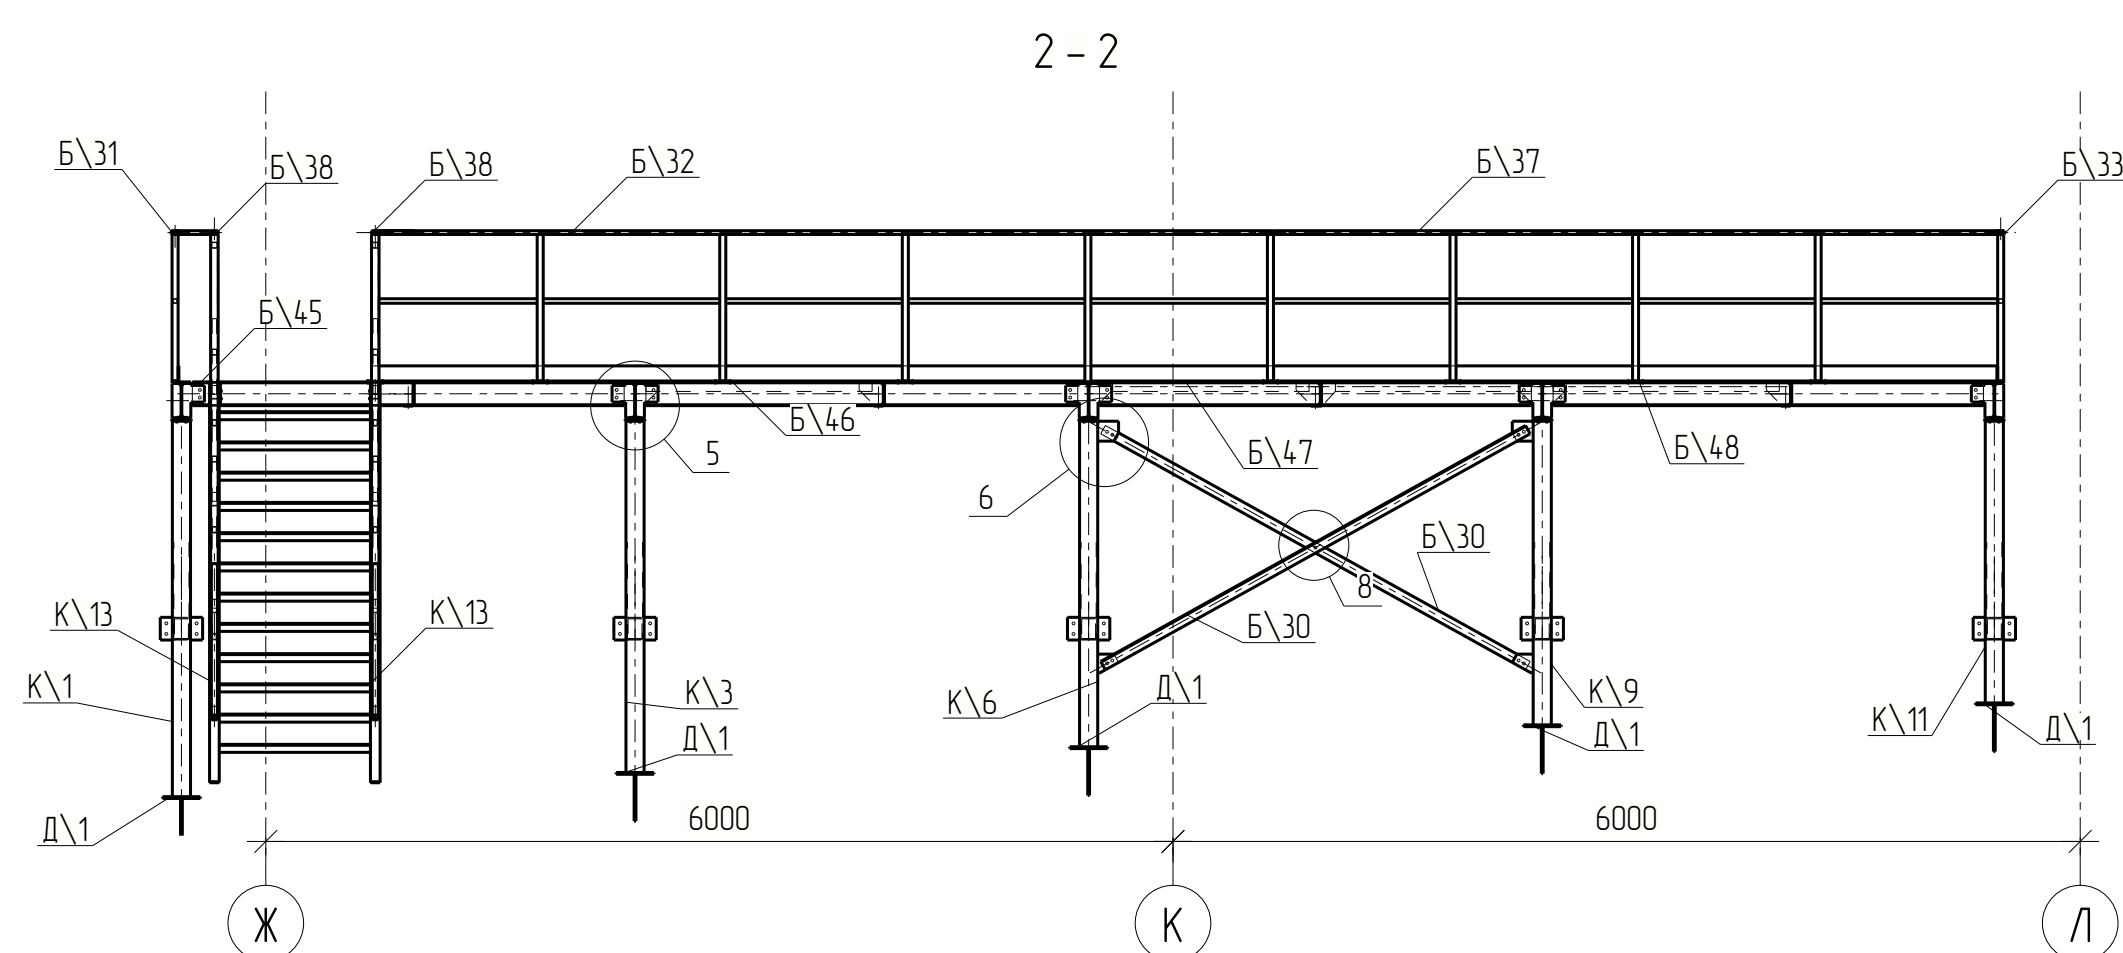
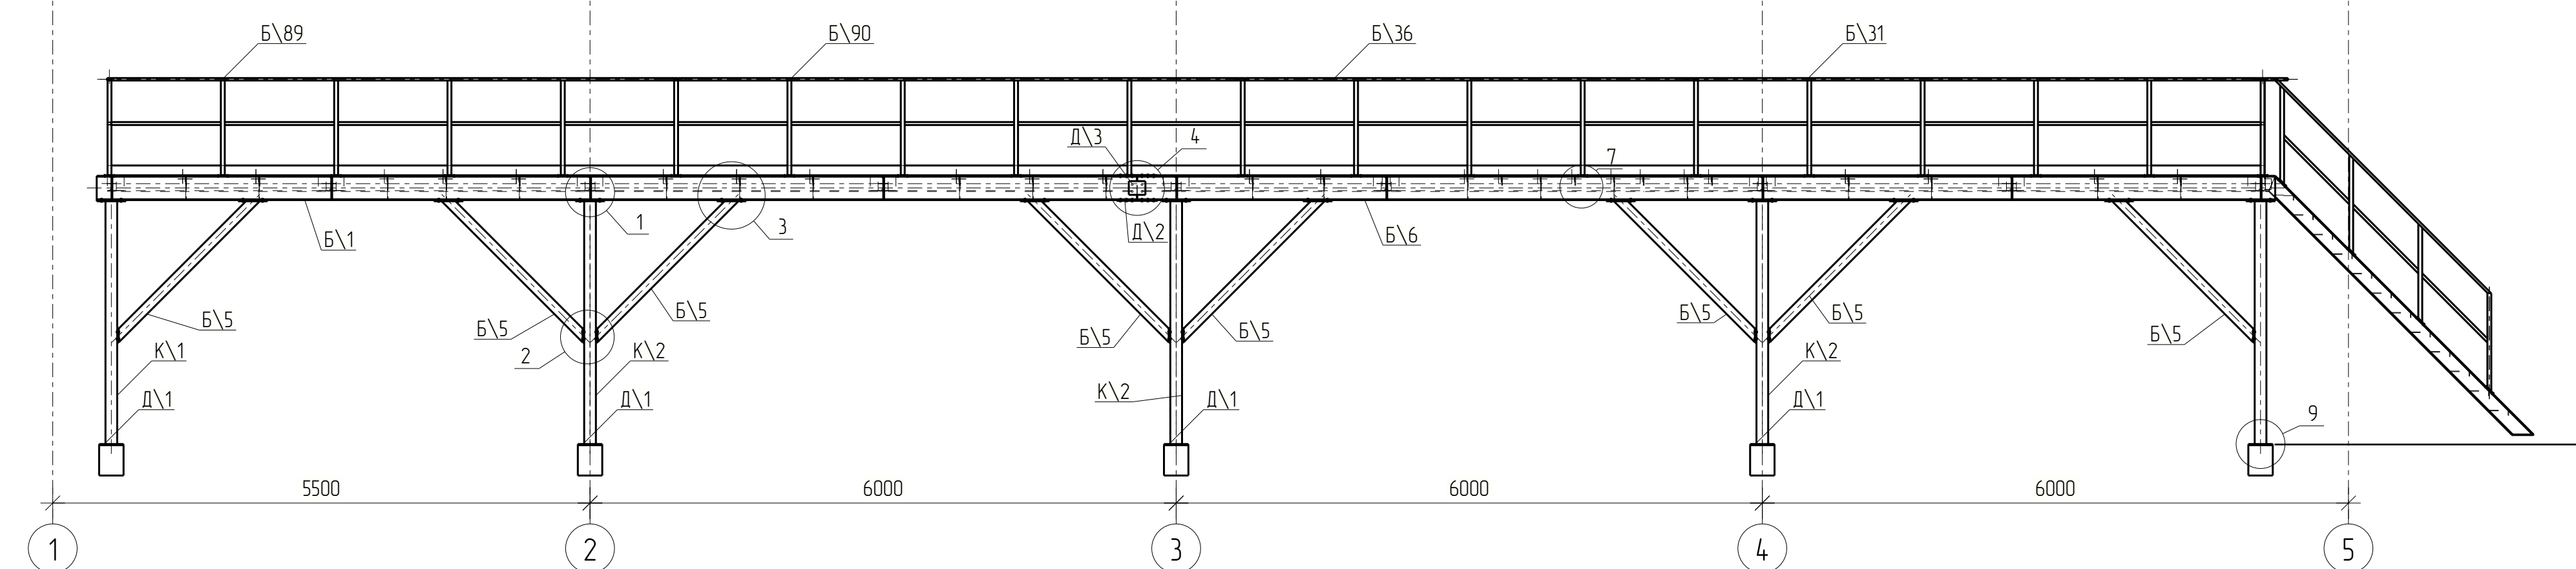
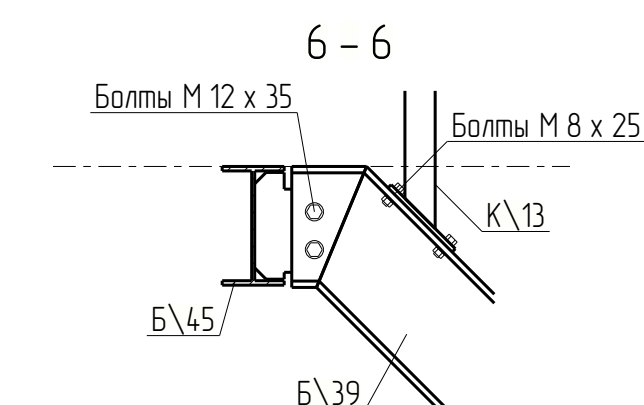


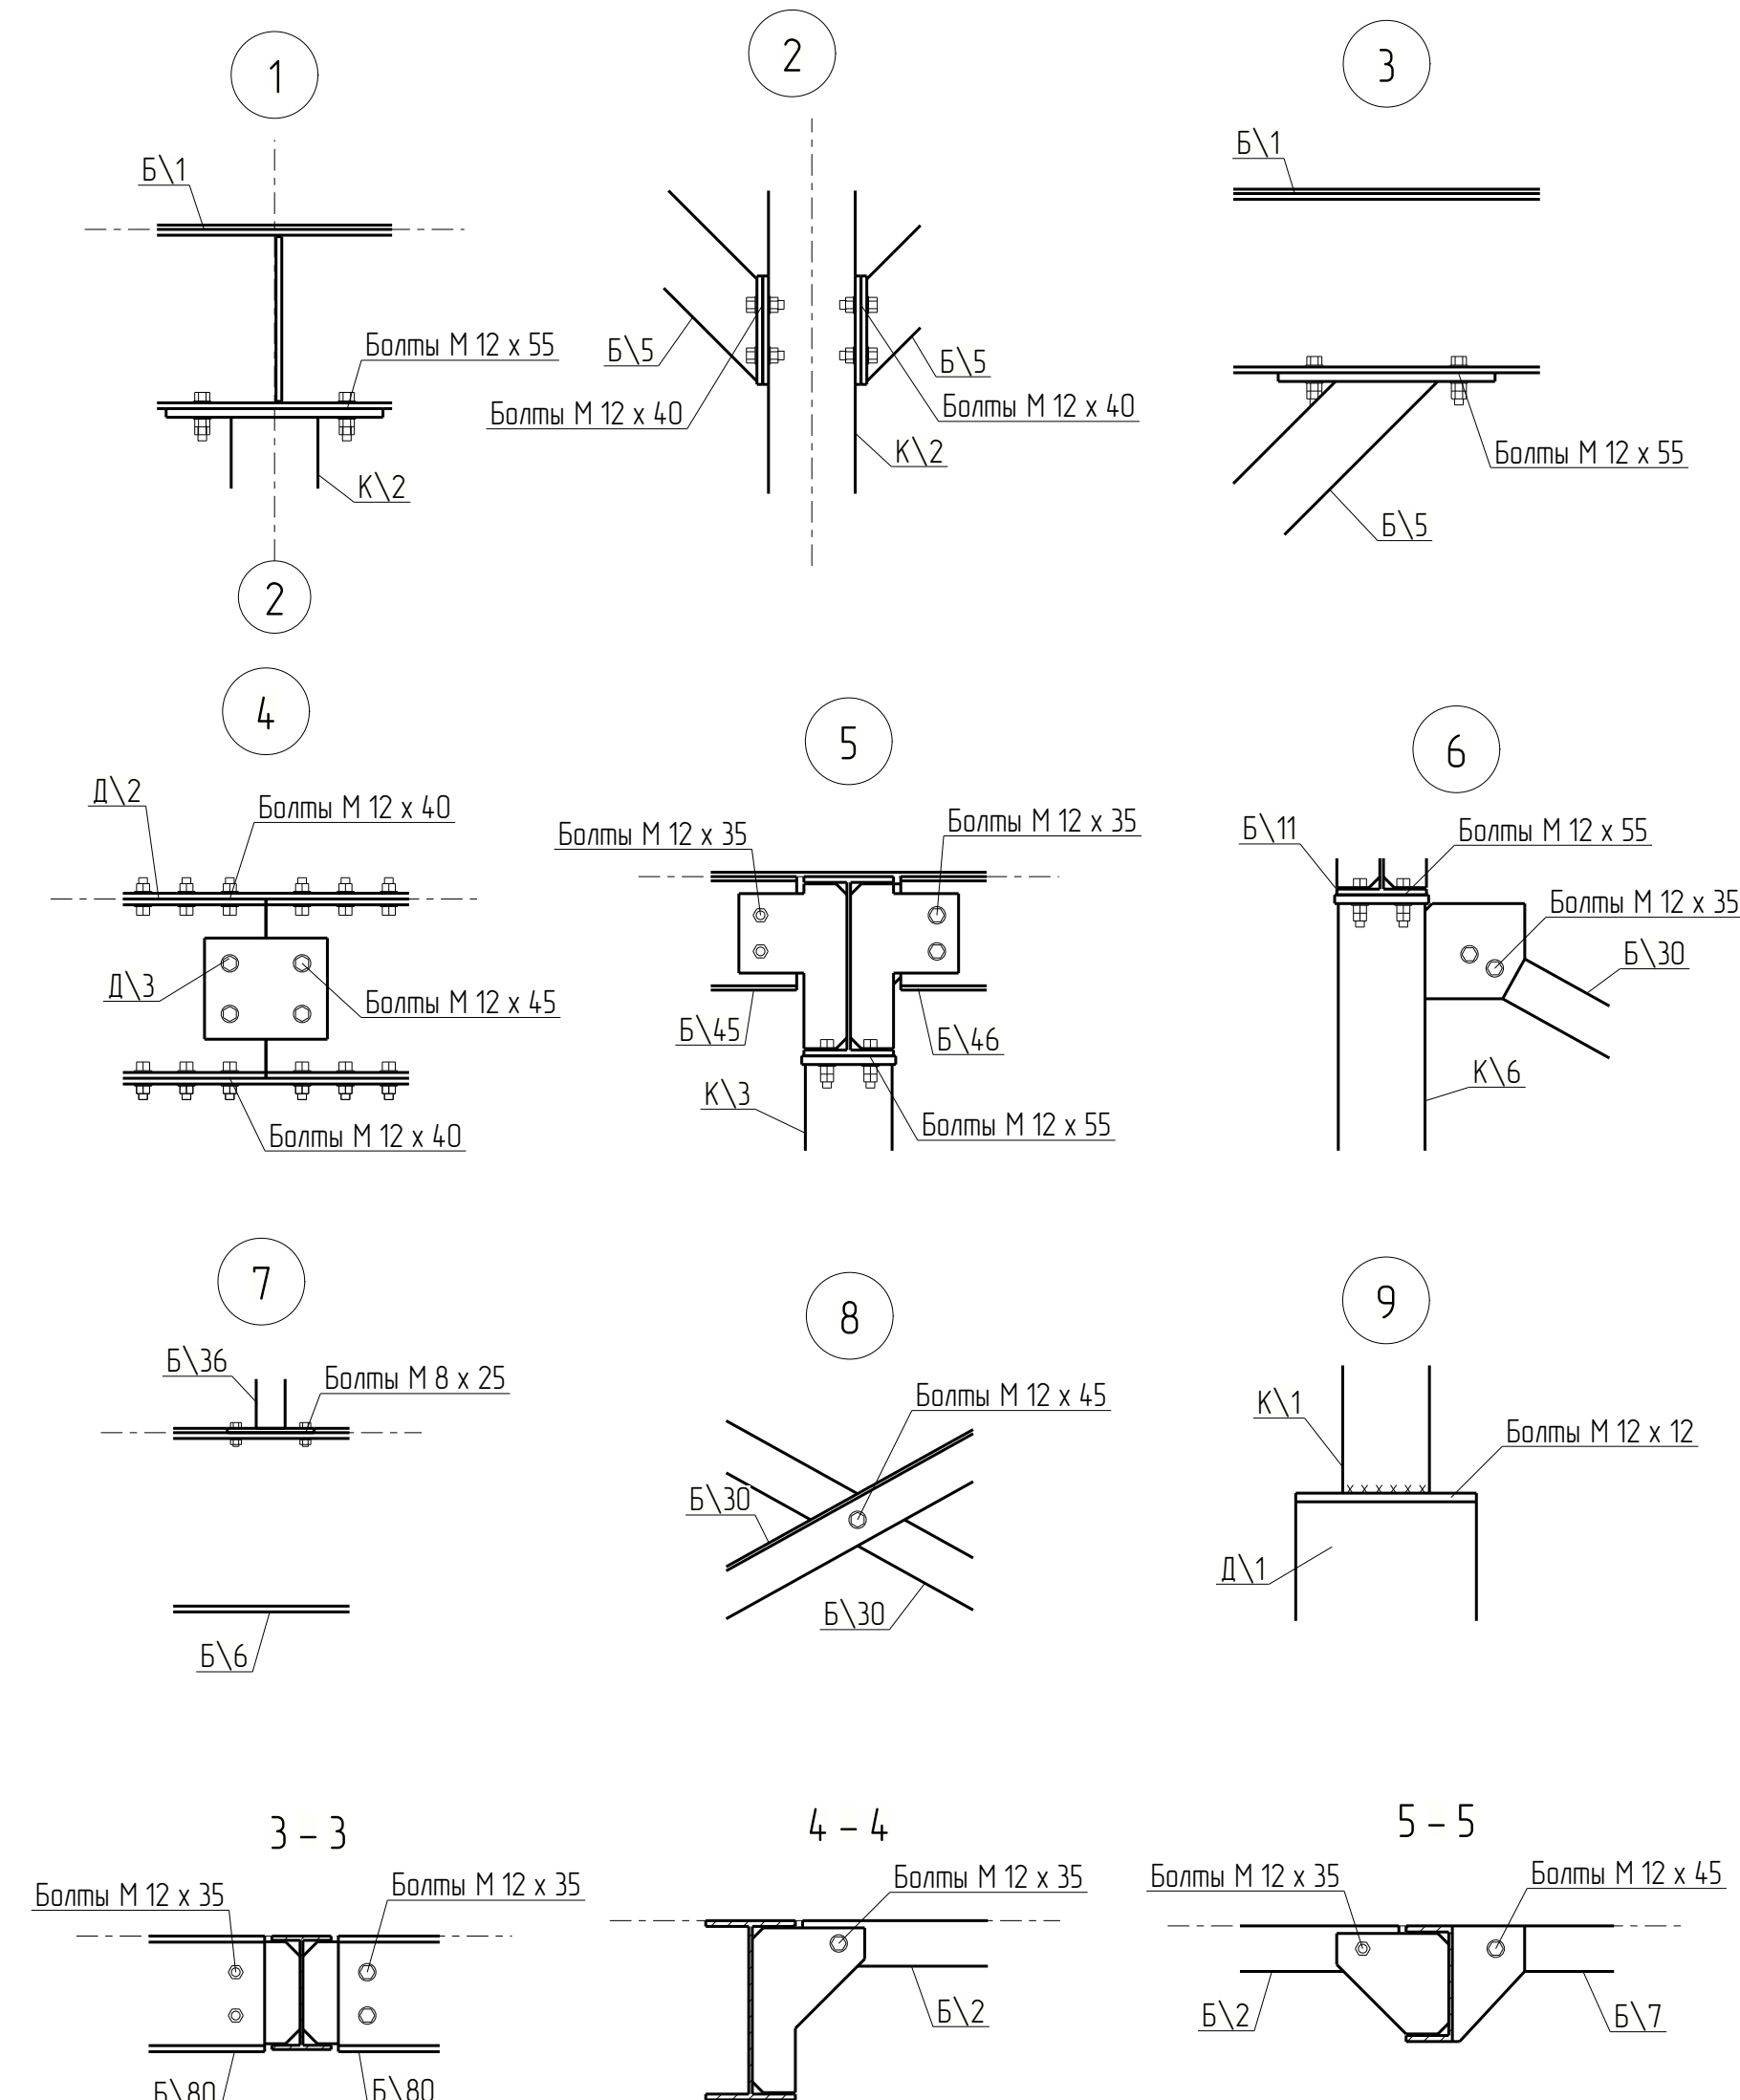

05-09/24

Площадка под ПВХ десертів на кровле	
-------------------------------------	--

Монтажная схема

Формат: А1

Изм.	Кол.уч	Лист	Идок.	Подпись	Дата
Гл.Инженер		Мухомов Д.В.			
Нач. отдела		Иванюк В.С.			
Н.Контр.		Иванюк В.С.			
Разработчик		Иванюк В.С.			