


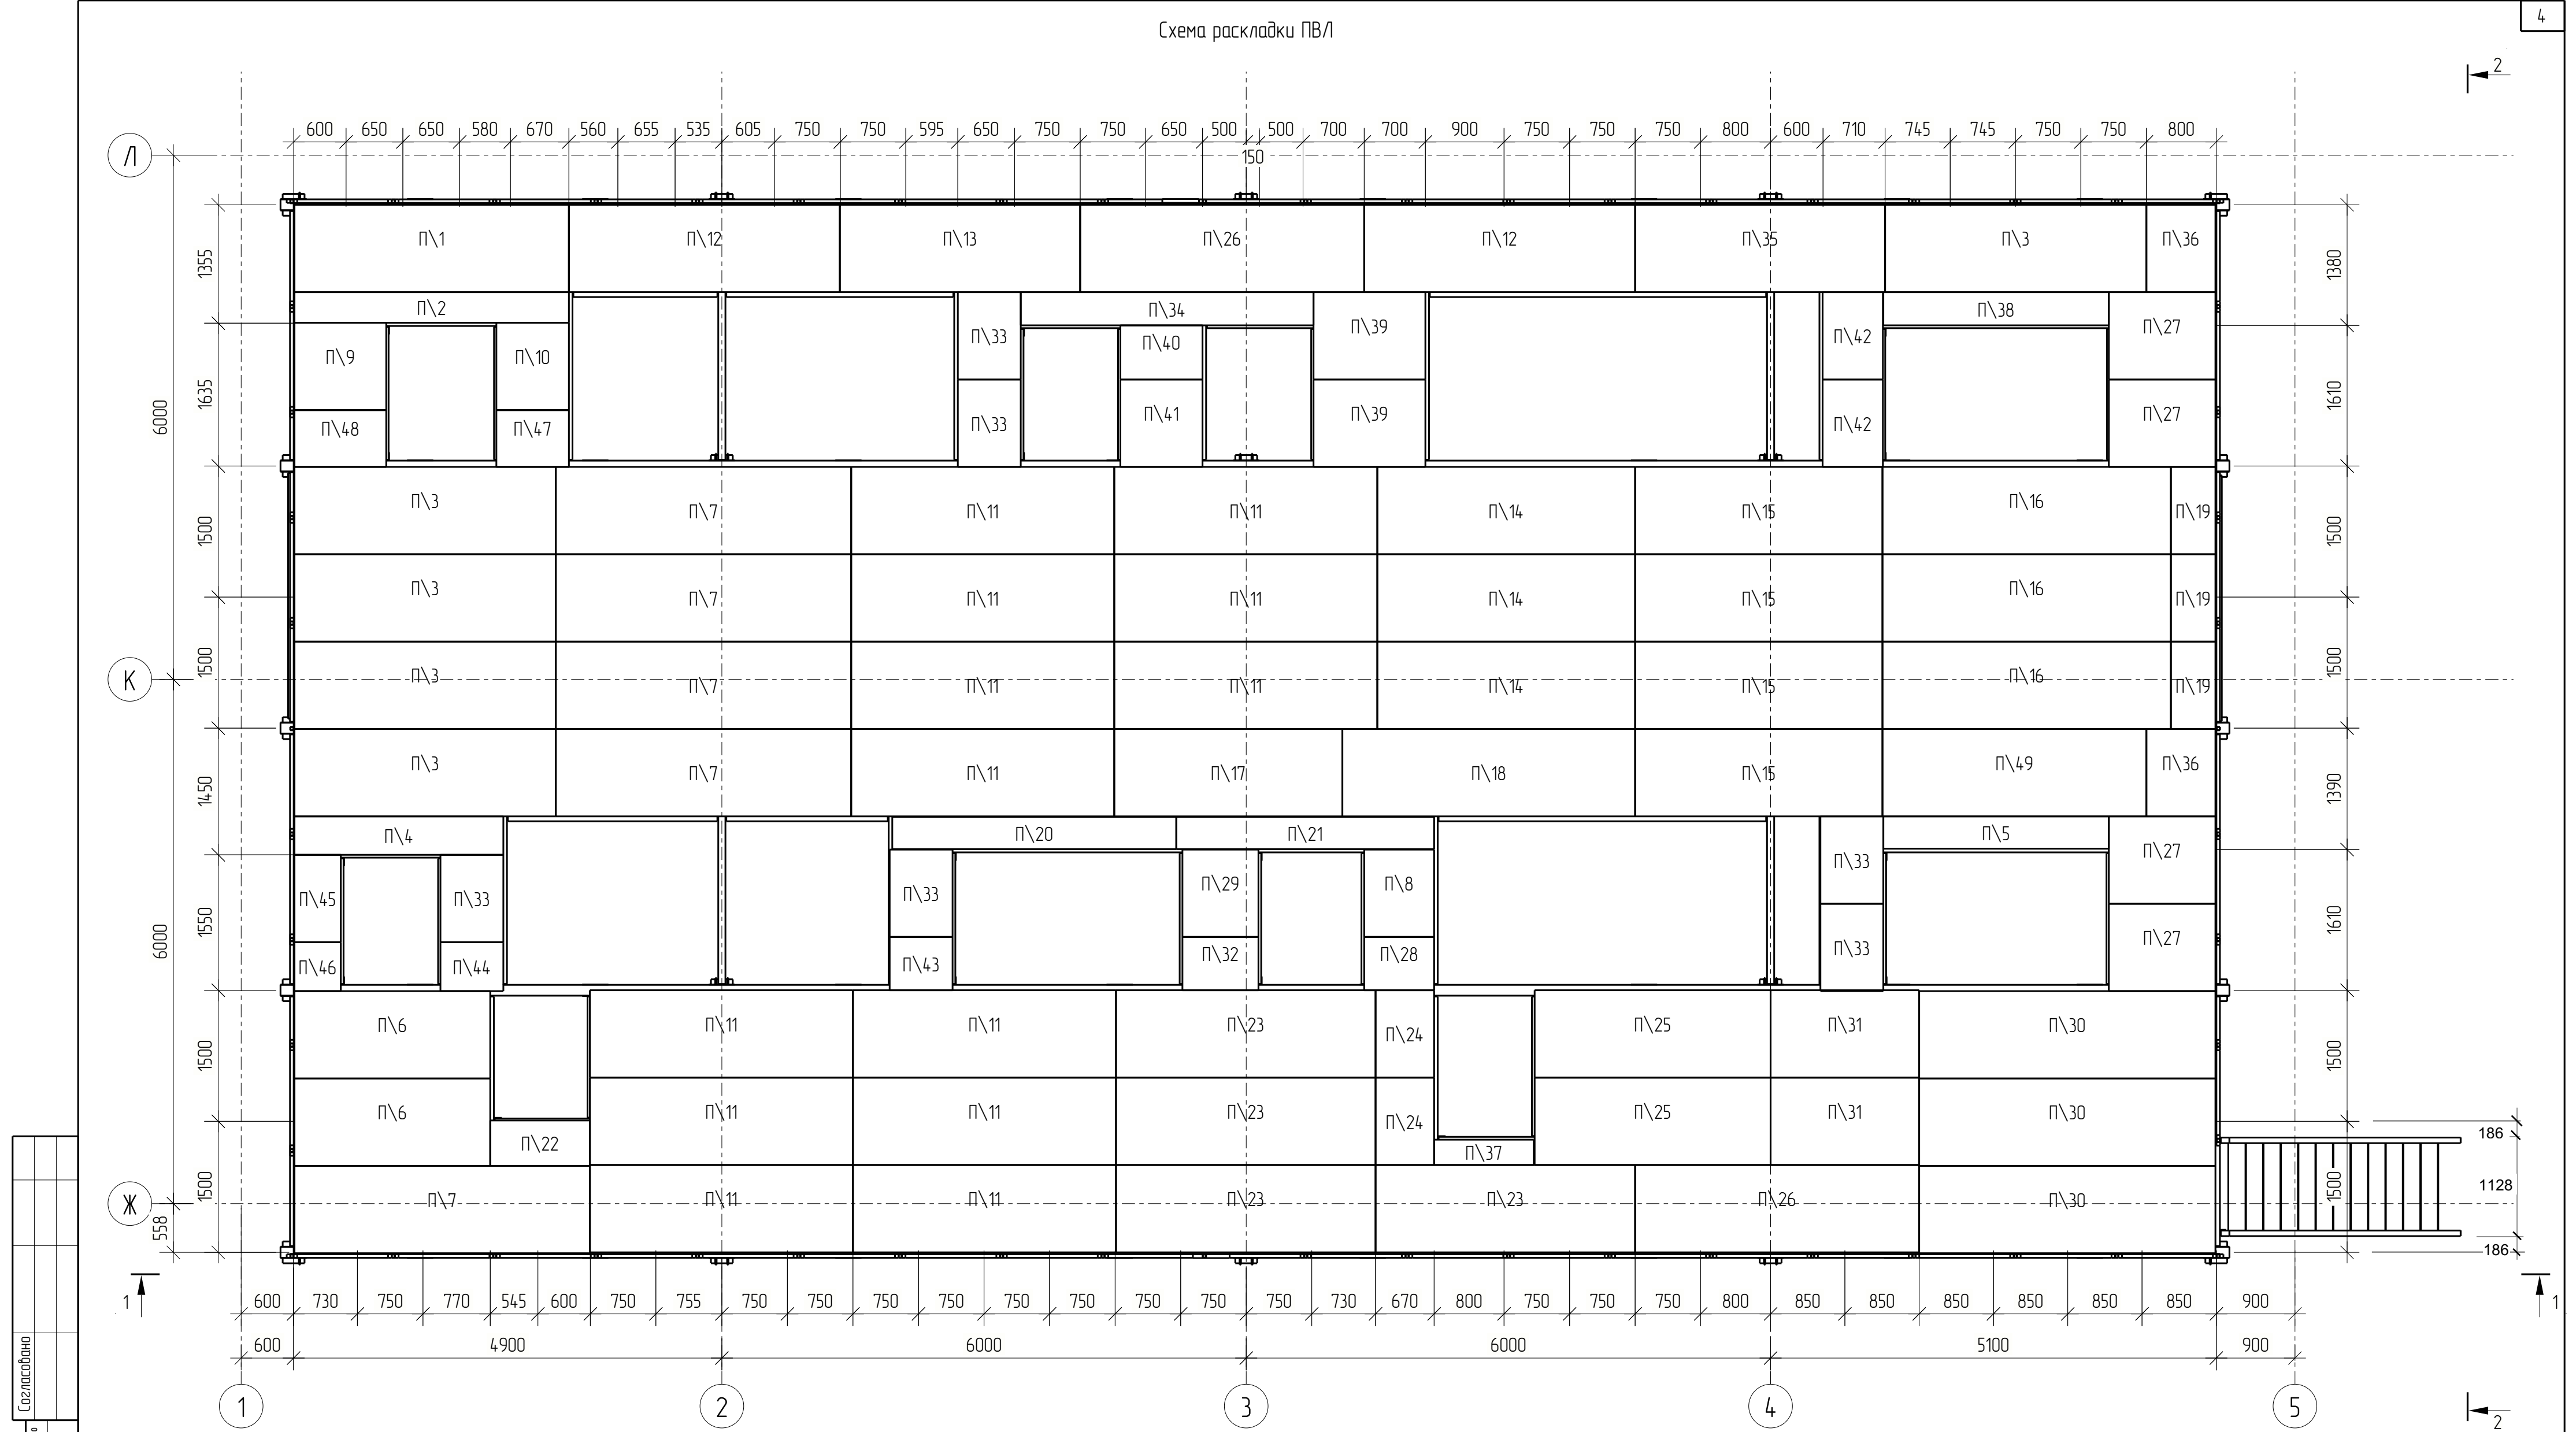

1. Общие данные см. Лист 1.

						05-09/24			
						Реконструкция здания главного корпуса с инвентарным № 110/С-97826 производственного филиала ОАО "Савушкин продукт" по адресу: г. Барановичи, ул. 50 лет БССР, 51/1			
Изм.	Кол.уч	Лист	Издок.	Подпись	Дата	Площадка под ПВУ десертов на кровле	Стадия	Лист	Листов
Гл.Инженер	Михняк Д.В.						С	4	
Нач. отдела	Иванюк В.С.								
Н.Контр.	Иванюк В.С.								
Разработал	Иванюк В.С.					Монтажная схема			